

**Karar Sayısı: 11802**

Ekli liste ile haritalarda kamulaştırma bilgileri ve güzergâhları gösterilen enerji nakil hatlarının yapımı amacıyla söz konusu güzergâhlara isabet eden taşınmazlarda elektrik dağıtım tesis yerlerinin mülkiyet şeklinde, hat emniyet sahalarının ise irtifak hakkı kurulmak suretiyle Türkiye Elektrik Dağıtım Anonim Şirketi Genel Müdürlüğü tarafından acele kamulaştırılmasına, 2942 sayılı Kamulaştırma Kanununun 27 nci maddesi gereğince karar verilmiştir.


17 Eylül 2026

Recep Tayyip ERDOĞAN
CUMHURBAŞKANI


17/9/2026 TARİHLİ VE 11802 SAYILI CUMHURBAŞKANI KARARININ EKİ

LİSTE VE HARİTALAR


SIRA NO	TESİS ADI	İLİ	UZUNLUK (km)	KAMULAŞTIRMA ALANI (m ²)	İRTİFAK ALANI (m ²)
1	Killik 1 ENH	Aksaray	0+368,82	25,11	2800,17
2	Yeni Köseali ENH	Aksaray ve Konya	14+559,26	2805,26	169252,94
3	A.2541.Şb.0057-Şemsettin Modüle Köyler Hattı Girdi-Çıktı Yapması ENH	Kocaeli	0+411,89	173,23	5573,02
4	Akmel Temizlik İlave TRP-TR5092 ENH	Kocaeli	2+583,83	770,18	15938,12
5	Şahinler RMU-Akçaova Çıkışı Yenileme Projesi ENH	Kocaeli	1+049,65	188,31	20710,43
6	Çomaklı - Maltsan ENH	Konya	4+757,70	1261,38	55332,71
7	Gökhüyük ADM Sulama Çıkışı ENH	Konya	26+137,87	4643,72	321003,59
8	Sarayönü - Bayramlı ENH	Konya	12+477,29	2862,20	148068,20
9	38 Nolu KÖK ve İrtibatları ENH	Nevşehir	2+986,52	625,34	33441,02
10	61 Nolu KÖK ve İrtibatları ENH	Nevşehir	3+559,62	1065,36	35993,66
11	Bajdarlık ADM Güney Altay ENH	Niğde	8+494,67	1716,91	101790,58
12	Başpınar Dereboğazı Yeraltı Şebeke Yenileme Projesi ENH	Sakarya	0+213,69	196,10	428,31

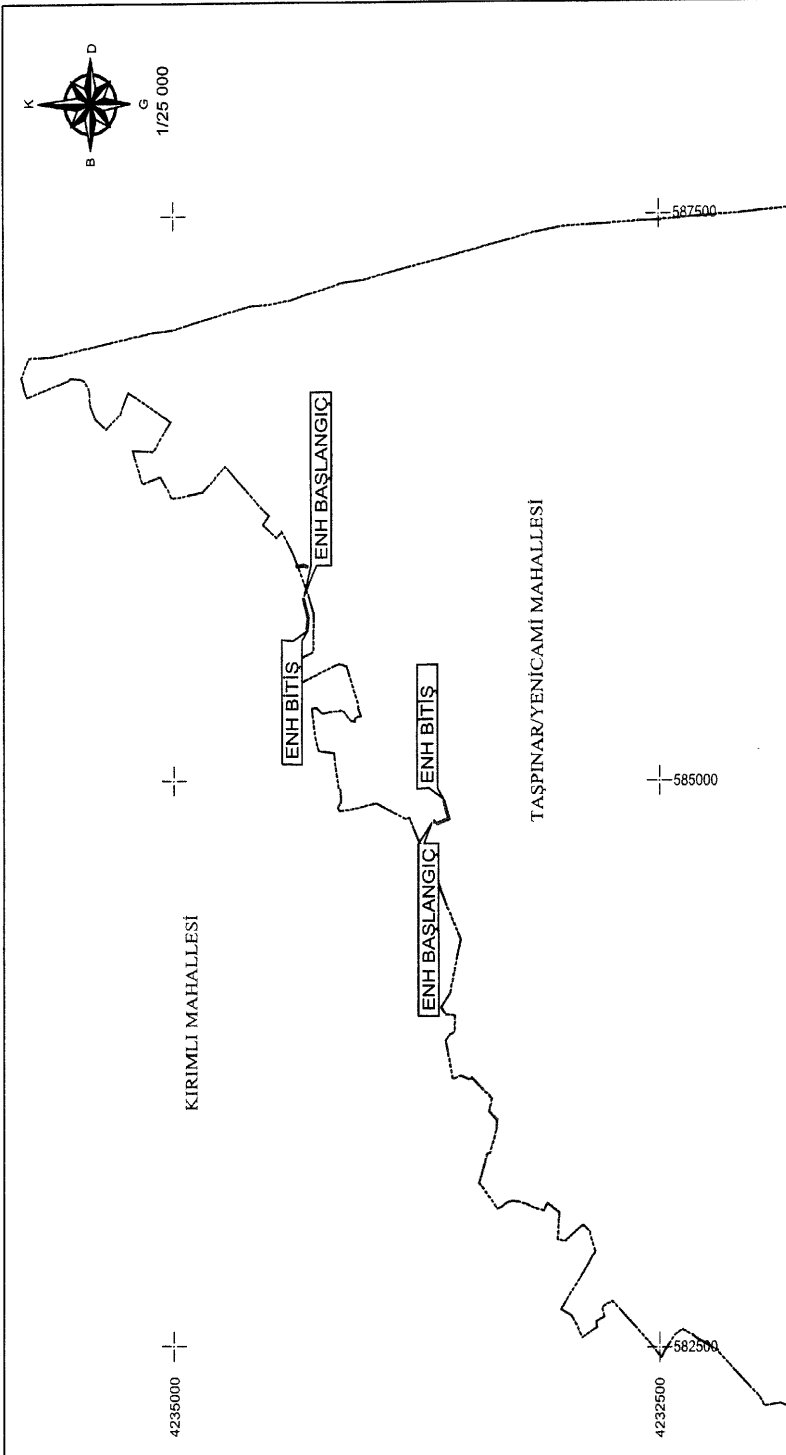



TÜRKİYE ELEKTRİK DAĞITIM A.Ş.	— TESİS EDİLECEK ENH ---- TESİS EDİLECEK YERALTI ■ TESİS EDİLECEK TRAFO	KILLIK 1 ENERJİ NAKİL HATTI KAMULAŞTIRMA YAPILACAK GÜZERGAH KBS ID: 102327	İLİ : AKSARAY İLÇESİ : MERKEZ MAHALLE : TAŞPINAR/YENİCAMI VE KIRIMLI	DATUM : ED50 D.NO : 36 İDİLİM ARALIĞI : 6° PAFTA : L31B3, L31C2
-------------------------------	--	---	---	--

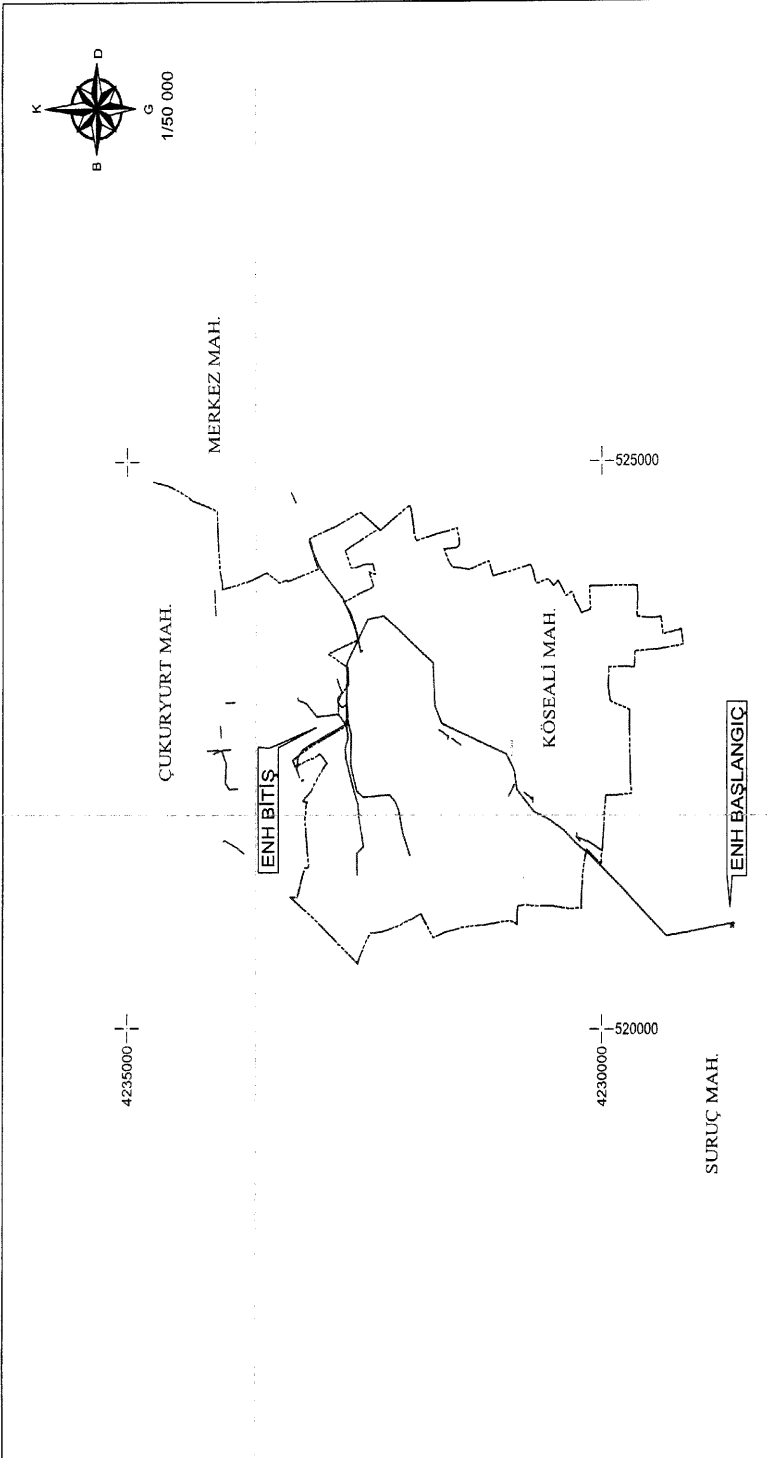


TÜRKİYE ELEKTRİK DAĞITIM AŞ.	TESİS EDİLECEK ENH TESİS EDİLECEK YERALTI TESİS EDİLECEK TRAFİ	YENİ KÖSEALİ ENERJİ NAKİL HATTI KAMULAŞTIRMA YAPILACAK GÜZERGAH KBS ID: 101773	İLİ: KONYA, AKSARAY İLÇESİ: KARATAY, ESKİL MAHALLE: SURUÇ, KÖSEALİ ÇUKURYURT VE MERKEZ	DATUM : ED50 D.NO : 36 DİLİM ARALIĞI : 6° PAFTA : L30-A3, L30-B4, L30-D2, L30-C1
------------------------------	---	--	--	---

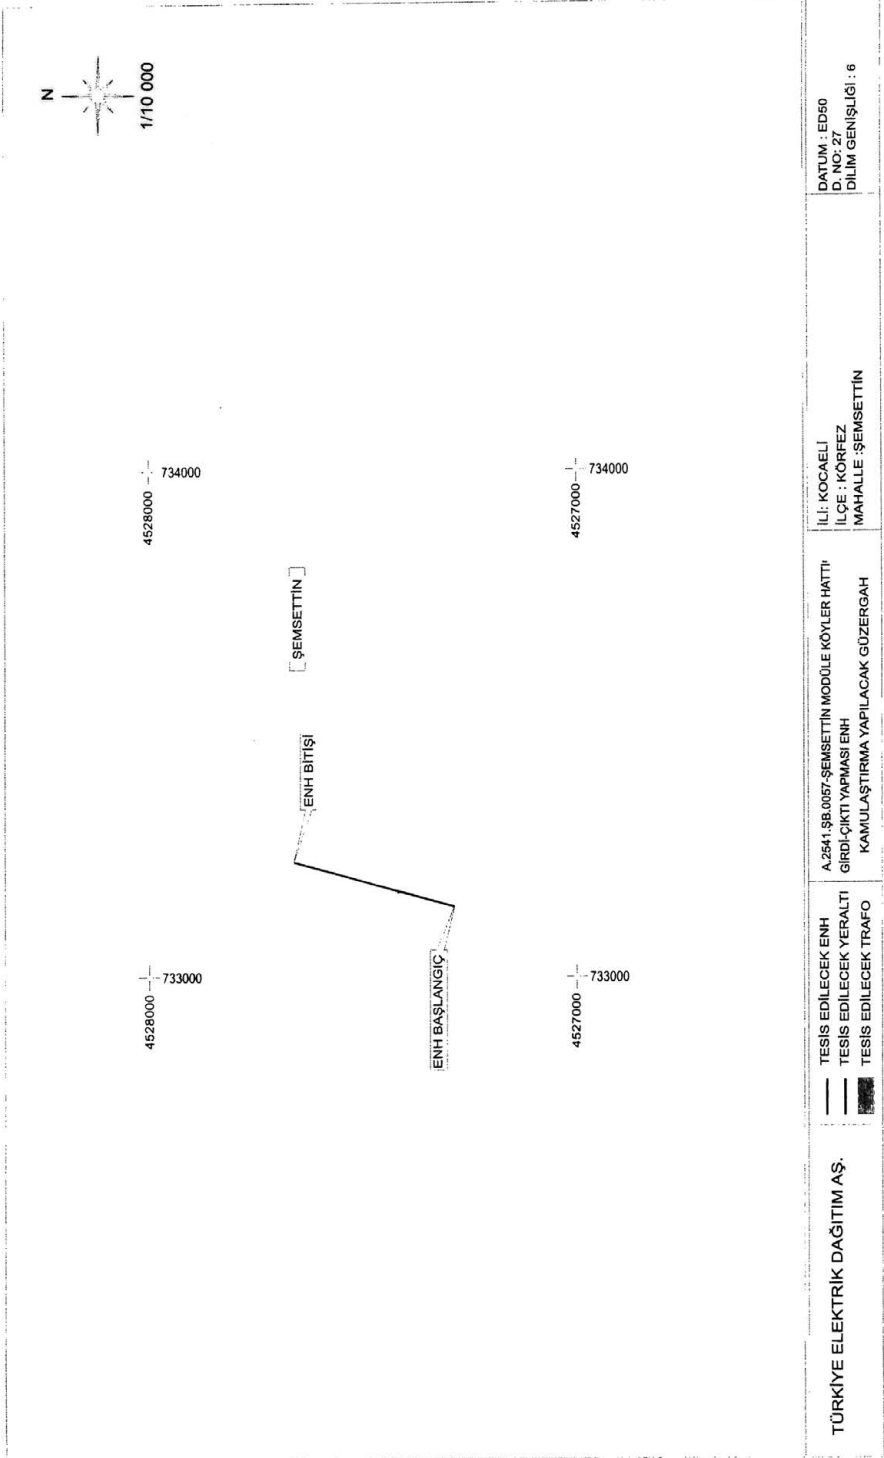


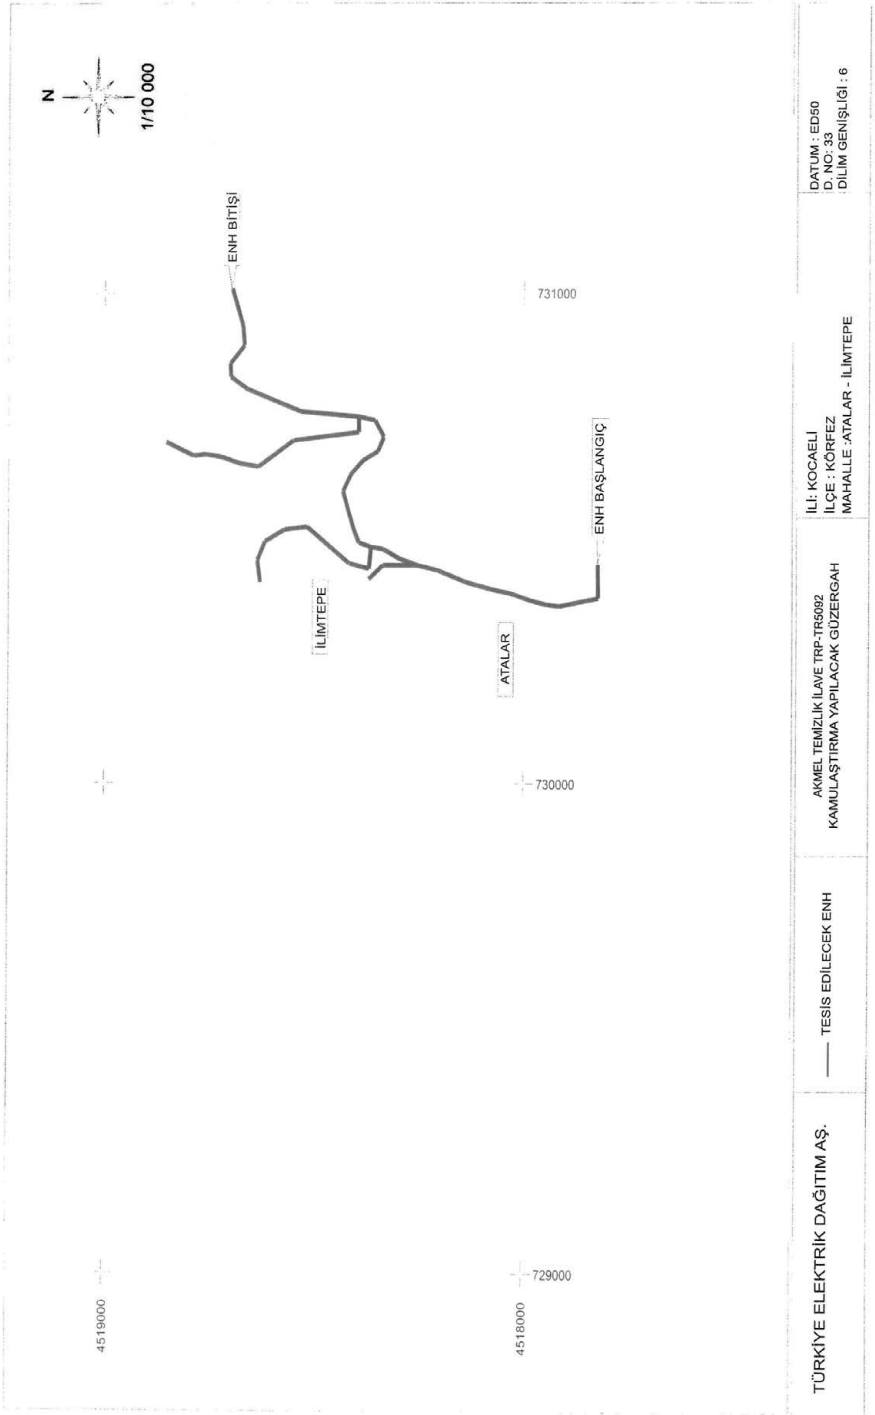

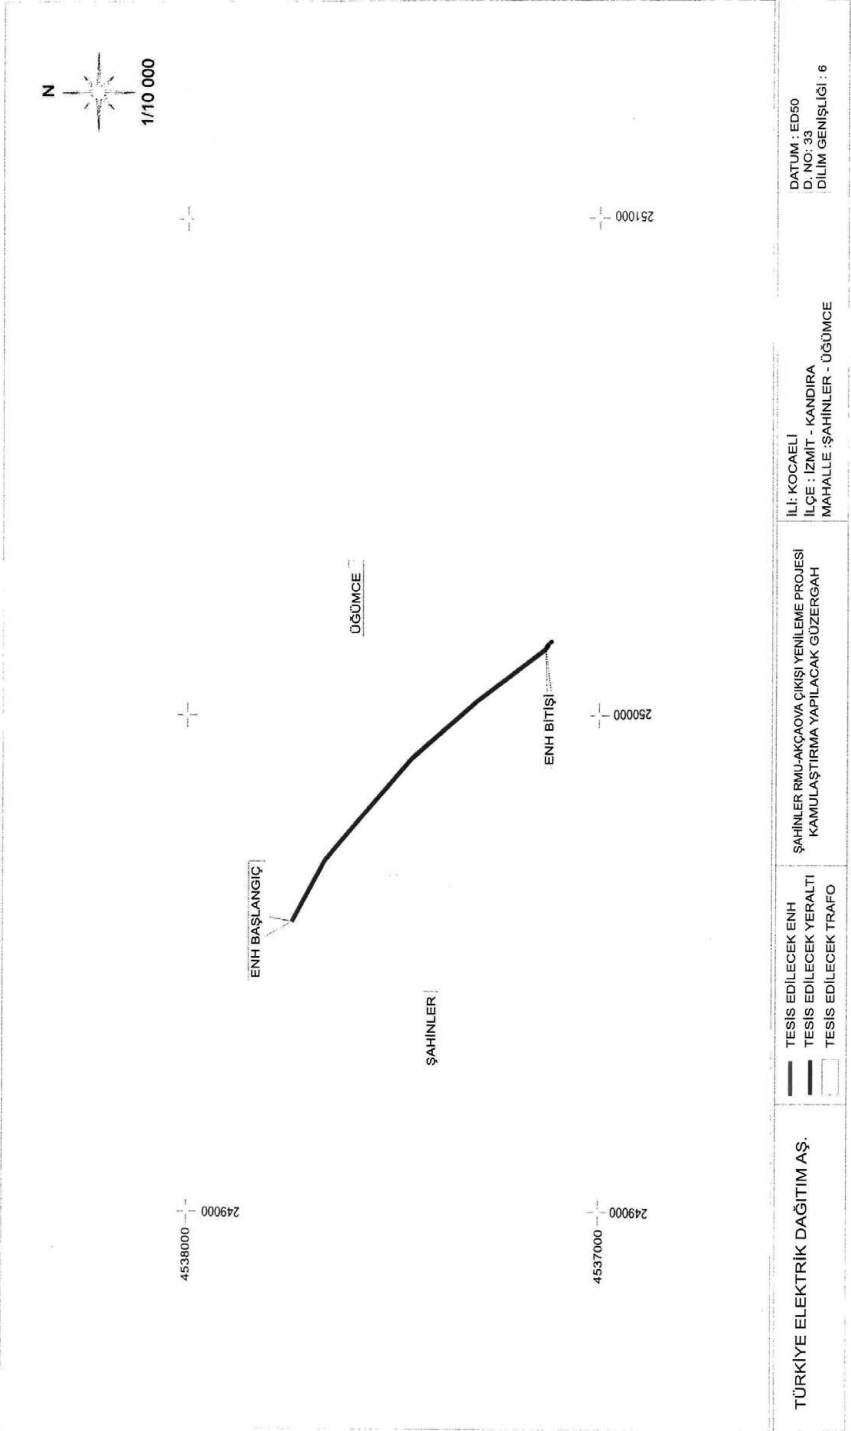


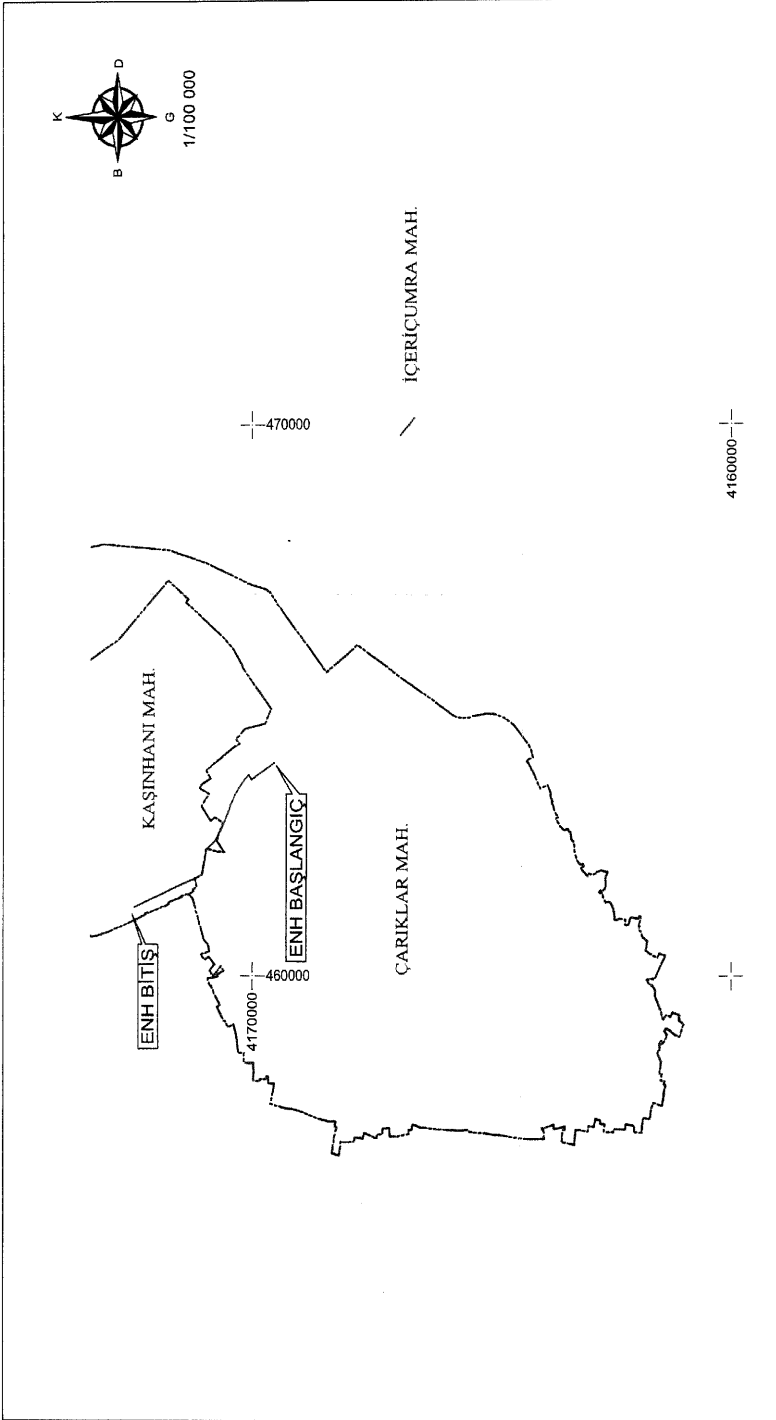


TÜRKİYE ELEKTRİK DAĞITIM AŞ.	TESİS EDİLECEK ENH TESİS EDİLECEK YERALTI TESİS EDİLECEK TRAFİ	ÇOMAKLI - MALTSAN ENERJİ NAKİL HATTI KAMULAŞTIRMA YAPILACAK GÜZERGAH KBS ID : 102278	İLİ : KONYA İLÇESİ : ÇUMRA, MERAM MAHALLESİ : İÇERİCUMRA, ÇARIKLAR, KAŞINHANI	DATUM : ED50 D.NO : 36 DİLİM ARALIĞI : 6° PAFTA : M29-D1, M29-D2
------------------------------	--	---	--	---

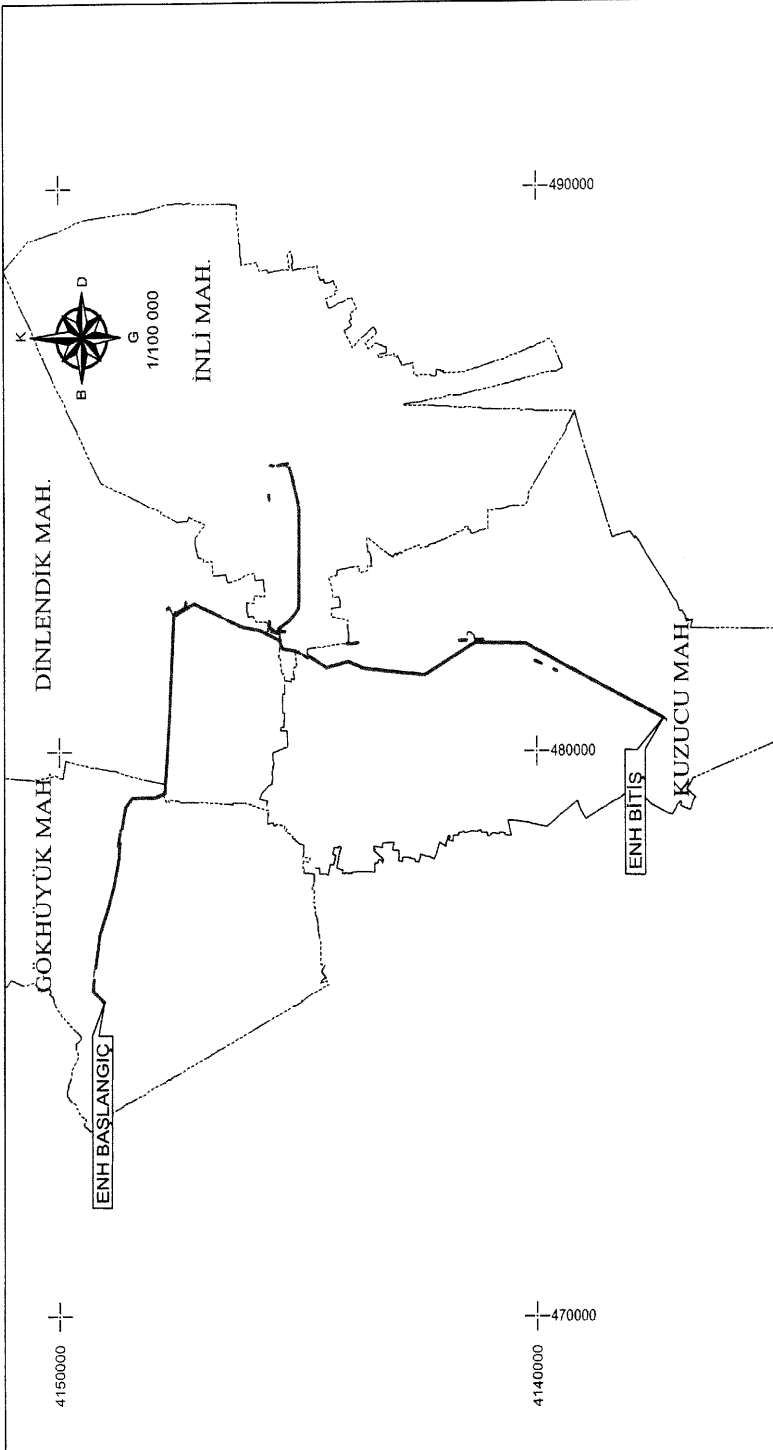


TÜRKİYE ELEKTRİK DAĞITIM A.Ş.	TESİS EDİLECEK ENH TESİS EDİLECEK YERALTI TESİS EDİLECEK TRAFİ	GÖKHÜYÜK ADM SULAMA ÇIKIŞI ENERJİ NAKİL HATTI KAMULAŞTIRMA YAPILACAK GÜZERGAH KBS ID: 102423	İLİ: KONYA İLÇESİ: ÇUMRA MAHALLE: GÖKHÜYÜK DİNLENDİK, İNİLİ, KUZUCU DATUM : ED50 D.NO : 36 DİLİM ARALIĞI : 6° PAFTA : N29A2,N29B1
-------------------------------	---	---	---

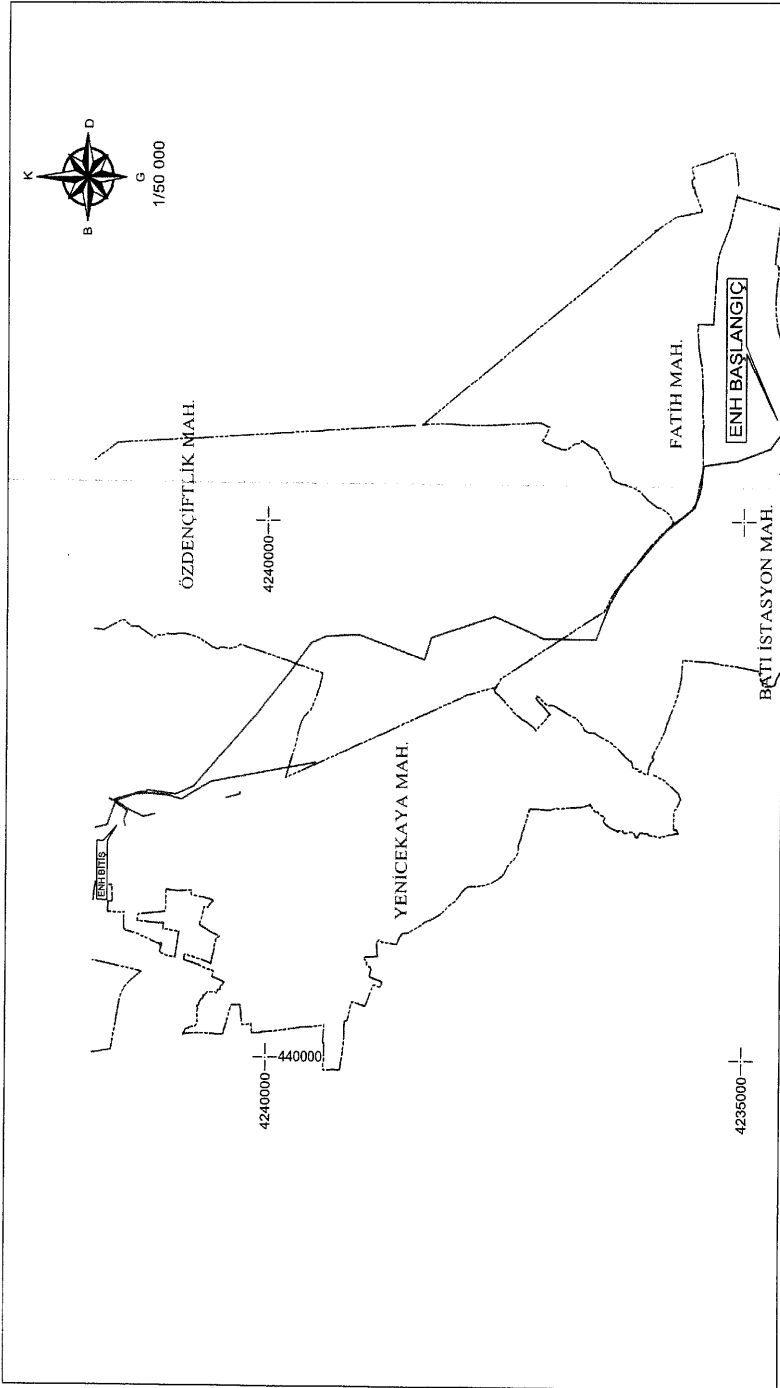


TÜRKİYE ELEKTRİK DAĞITIM AŞ.	— TESİS EDİLECEK ENH — TESİS EDİLECEK YERALTI ■ TESİS EDİLECEK TRAFO	SARAYÖNÜ - BAYRAMLI ENERJİ NAKİL HATTI KAMULAŞTIRMA YAPILACAK GÜZERGAH KBS ID : 102436	İLİ: KONYA İLÇESİ : SARAYÖNÜ MAHALLESİ : BATI İSTASYON, FATİH, ÖZDENÇİFTLİK, YENİCEKAYA	DATUM : ED50 D.NO : 36 DİLİM ARALIĞI : 6° PAFTA : L28-B4, L28-B3
------------------------------	---	--	---	--

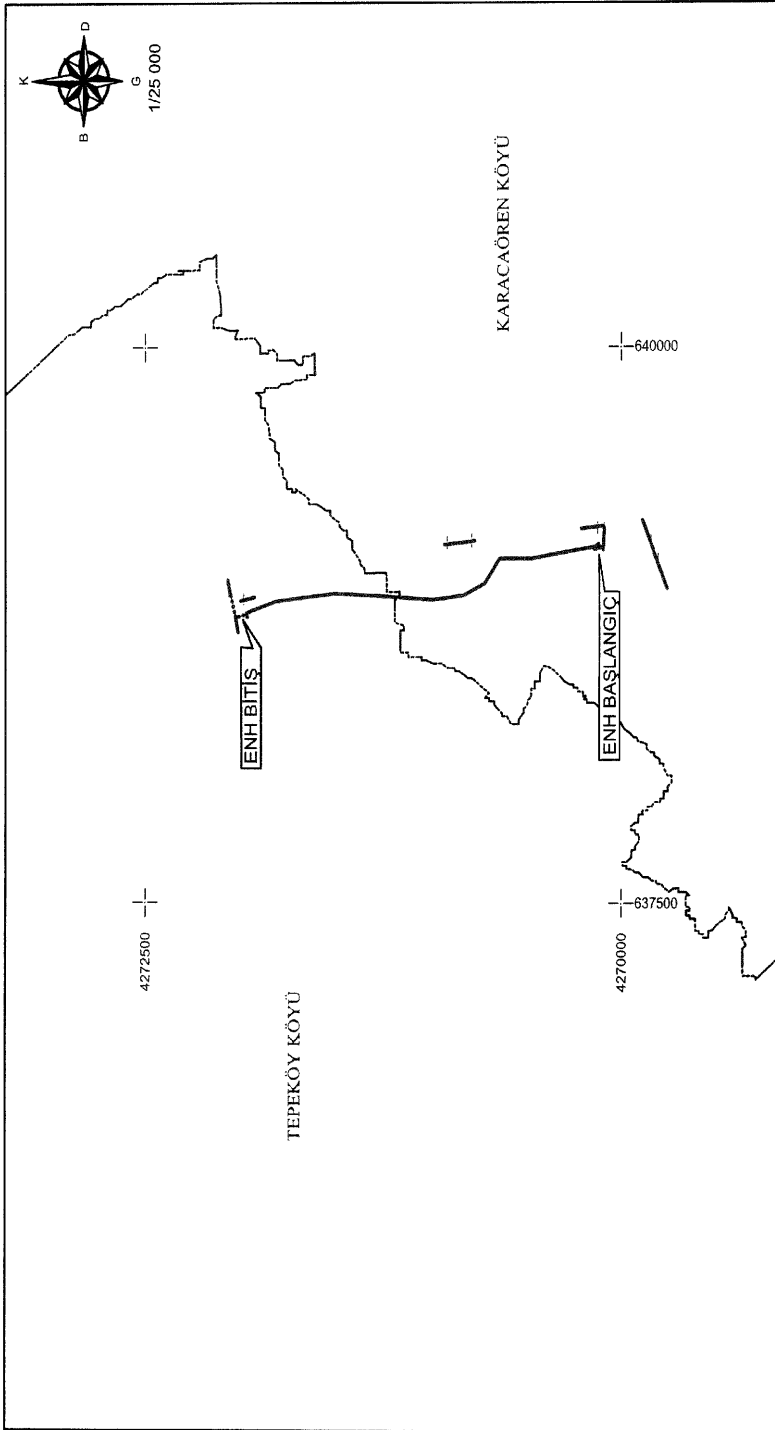

TÜRKİYE ELEKTRİK DAĞITIM AŞ.	TESİS EDİLECEK ENH TESİS EDİLECEK YERALTI TESİS EDİLECEK TRAFİ	38 NOLU KÖK VE İRTİBATLARI ENERJİ NAKİL HATTI KAMULAŞTIRMA YAPILACAK GÜZERGAH KBS ID : 102315	İLİ: NEVŞEHİR İLÇESİ : ACIGÖL KÖYÜ : KARACAÖREN VE TEPEKÖY	DATUM : ED50 D.NO : 36 DİLİM ARALIĞI : 6° PAFTA : K33D4
------------------------------	---	--	---	--

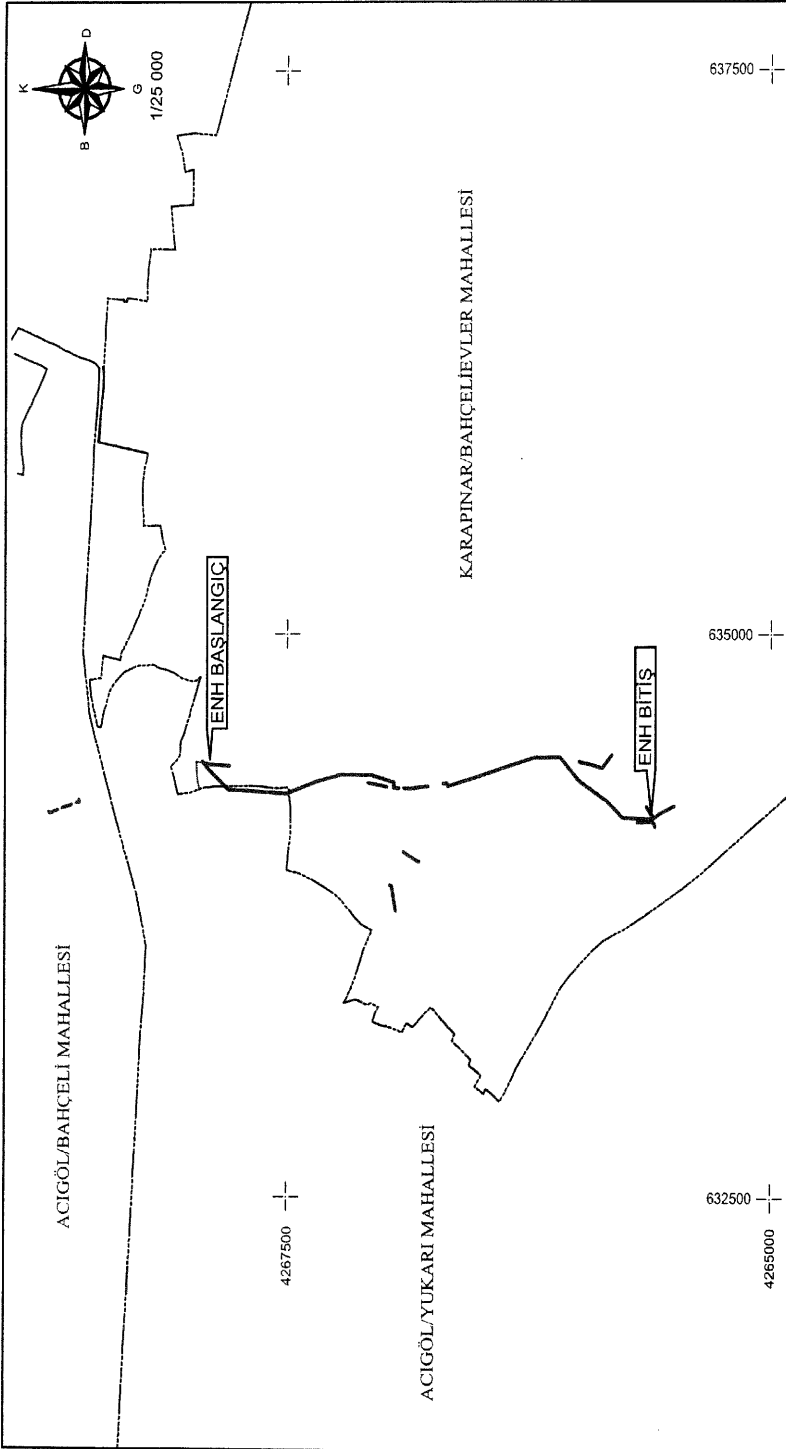

TÜRKİYE ELEKTRİK DAĞITIM AŞ	— TESİS EDİLECEK ENH - - - TESİS EDİLECEK YERALTI ■ TESİS EDİLECEK TRAFİ	61 NOLU KÖK VE İRTİBATLARI ENERJİ NAKİL HATTI KAMULAŞTIRMA YAPILACAK GÜZERGAH KBS ID : 102489	İLİ: NEVŞEHİR İLÇESİ : ACIGÖL MAH. : ACIGÖL/BAHÇELİ, ACIGÖL/YUKARI VE KARAPINAR/BAHÇELİEVLER	DATUM : ED50 D.NO : 36 DİLİM ARAĞIĞI : 6° PAFTA : K33-D4
-----------------------------	---	--	---	--

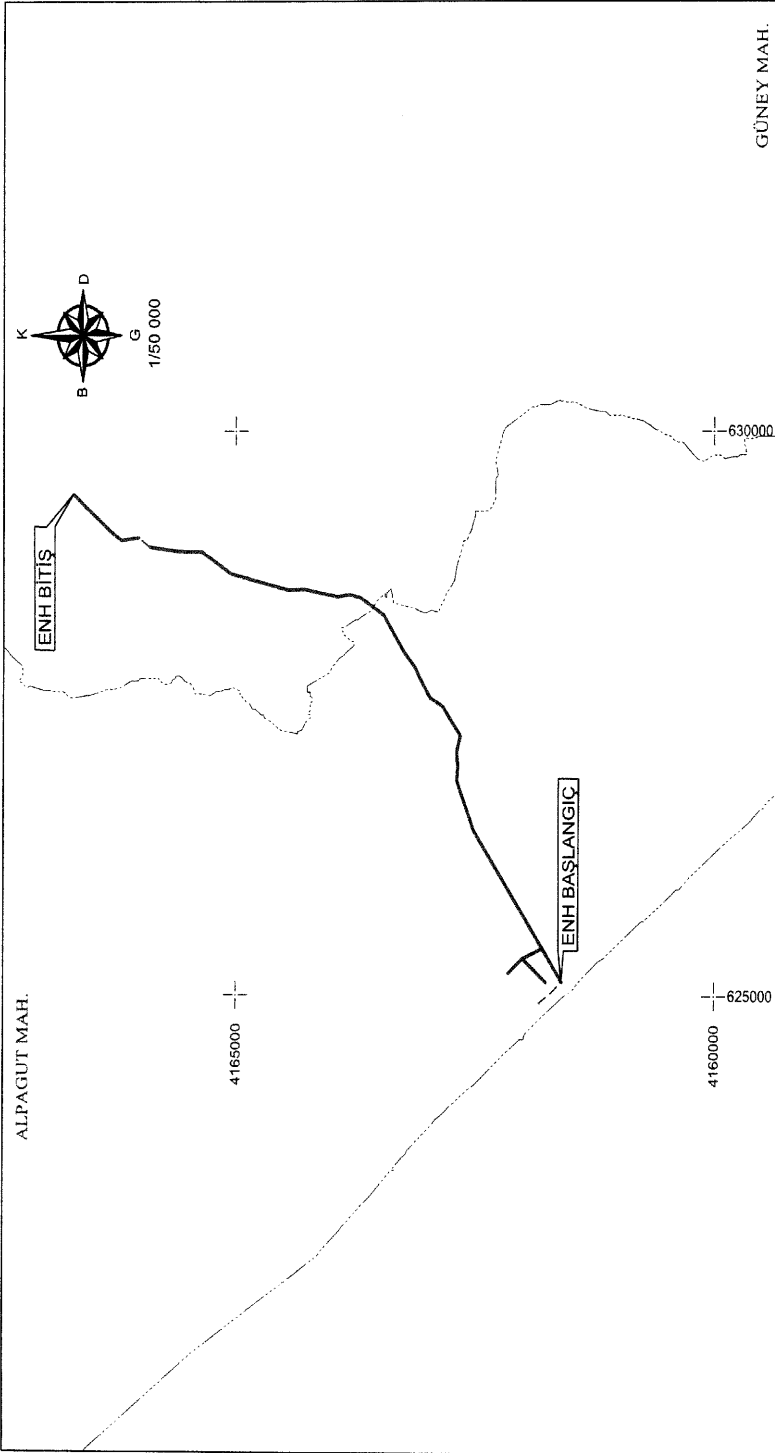

TÜRKİYE ELEKTRİK DAĞITIM A.Ş.	TESİS EDİLECEK ENH TESİS EDİLECEK YERALTI TESİS EDİLECEK TRAFO	BAJDARLIK ADM GÜNEY ALTAY ENERJİ NAKİL HATTI KAMULAŞTIRMA YAPILACAK GÜZERGAH KBS ID: 15005	İL: NİĞDE İLÇESİ: ULUKIŞLA MAHALLE: ALPAGUT, GÜNEY	DATUM : ED50 D.NO : 36 DİLİM ARALIĞI : 6° PAFTA : M32-C3,M32-C2
-------------------------------	---	---	--	--

**Karar Sayısı: 11803**

Batman İli, Merkez İlçesi, Tilmis (Akça) köyü sınırları içerisinde bulunan ve ekli listede bulunduğu yer ile ada ve parsel numarası belirtilen taşınmazların, “İluh Deresi By-Pass Hattı ile Çay Deresi Deplase Hattı Projesi”nin gerçekleştirilmesi amacıyla Batman İl Özel İdaresi tarafından acele kamulaştırılmasına, 2942 sayılı Kamulaştırma Kanununun 27 nci maddesi gereğince karar verilmiştir.

17 Eylül 2026

Recep Tayyip ERDOĞAN
CUMHURBAŞKANI