

**Karar Sayısı: 11863**


Ekli liste ile haritalarda kamulaştırma bilgileri ve güzergâhları gösterilen enerji nakil hatlarının yapımı amacıyla söz konusu güzergâhlara isabet eden taşınmazlarda elektrik dağıtım tesis yerlerinin mülkiyet şeklinde, hat emniyet sahalarının ise irtifak hakkı kurulmak suretiyle Türkiye Elektrik Dağıtım Anonim Şirketi Genel Müdürlüğü tarafından acele kamulaştırılmasına, 2942 sayılı Kamulaştırma Kanununun 27 nci maddesi gereğince karar verilmiştir.

9 Ekim 2026


Recep Tayyip ERDOĞAN
CUMHURBAŞKANI


9/10/2026 TARİHLİ VE 11863 SAYILI CUMHURBAŞKANI KARARININ EKİ
LİSTE VE HARİTALAR

SIRA NO	TESİS ADI	İLİ	UZUNLUK (km)	KAMULAŞTIRMA ALANI (m ²)	İRTİFAK ALANI (m ²)
1	Çardak - Sazköy DM - Çaltı TR-1 - Güneşli GES DM Arası ENH	Denizli	11+012,98	813,50	160.559,23
2	Çivril TM-Yiğit DM Arası ENH ve DM Tesis İşİ ENH	Denizli	9+063,70	1.880,58	103.808,46
3	Nazar-Sarkuysan GES ENH	Diyarbakır	16+896,11	5.621,96	184.031,14
4	Sultanice KÖK-Gülçavuş Sahil DM1-TR1 ENH	Edirne	3+363,37	414,57	46.809,96
5	Harmanaltı DM-Tosunburnu KÖK ENH	Kırşehir	13+481,20	1.339,85	163.909,63
6	66 Nolu KÖK - Sarıç DM ENH	Konya	10+063,24	1.809,62	120.545,46
7	Fevziye KÖK Bozan ENH	Konya	17+752,34	1.809,63	221.410,81
8	Karaömerler DM ENH	Konya	11+352,84	1.516,50	136.727,18
9	Kargacı Servili Pınarözü ENH	Konya	10+961,50	1.178,60	106.300,71
10	Zincirli Sulama ENH	Konya	14+632,88	2.329,57	172.395,24
11	Boğaz ADM ve İrtibatları ENH	Nevşehir	8+780,97	2.203,10	94.370,41
12	Hamzalı GES KÖK-Hamzalı MOD ENH	Nevşehir	9+030,96	2.578,20	106.076,36
13	Özay İM ve İrtibatları ENH	Nevşehir	2+254,55	821,34	28.915,24
14	Yeni Kurt DM ENH	Niğde	3+980,35	433,57	42.452,31
15	Jandarma Kabin - TOKİ DM Şebeke Yenileme Projesi ENH	Sakarya	0+918,43	317,14	1.837,44
16	BİM Viranşehir GES ENH	Şanlıurfa	20+831,83	8.867,71	398.856,78
17	Central GES İlave DM ve 400 KVA TR DM ENH	Trabzon	0+598,68	132,48	3.629,59

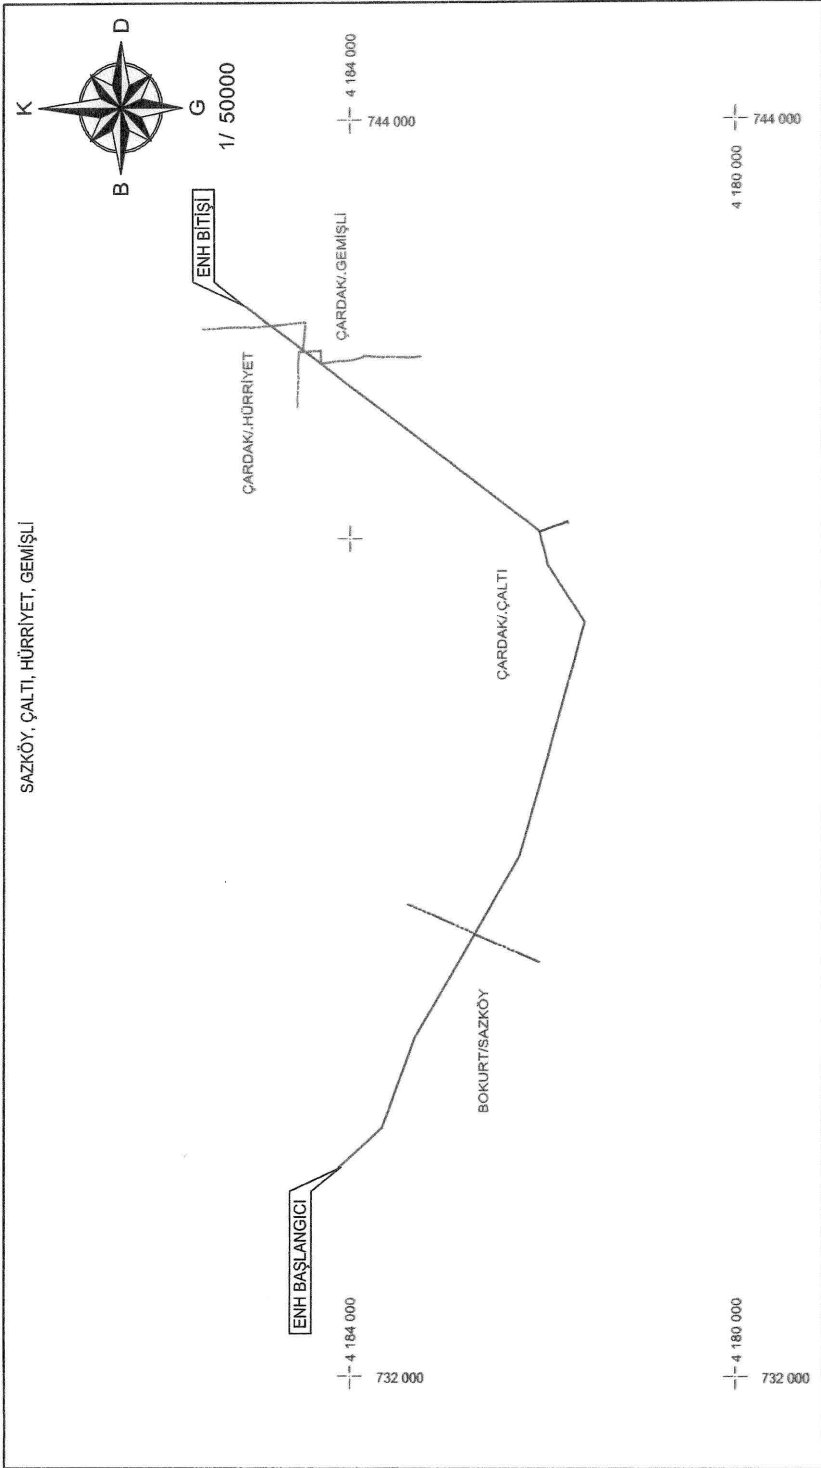



DATUM : ED00 DİLİM NO : 35 DİLİM GENİŞLİĞİ : 5°	İLİ : DENİZLİ İLÇESİ : BOZKURT, ÇARDAK MAHALLESİ : SAZKÖY, ÇALTI, HÜRRİYET, GEMİŞLİ	ÇARDAK - SAZKÖY DM - ÇALTI TR-1 - GÜNEŞİTİ GES DM ARASI ENERJİ NAKİL HATTI KAMULAŞTIRMA YAPILACAK GÜZERGAH KİŞİ ID :	TÜRKiYE ELEKTRİK DAĞITIM A.Ş. TESIS EDİLECEK ENH TESIS EDİLECEK YERALTI TESIS EDİLECEK TRAFO
---	---	---	---

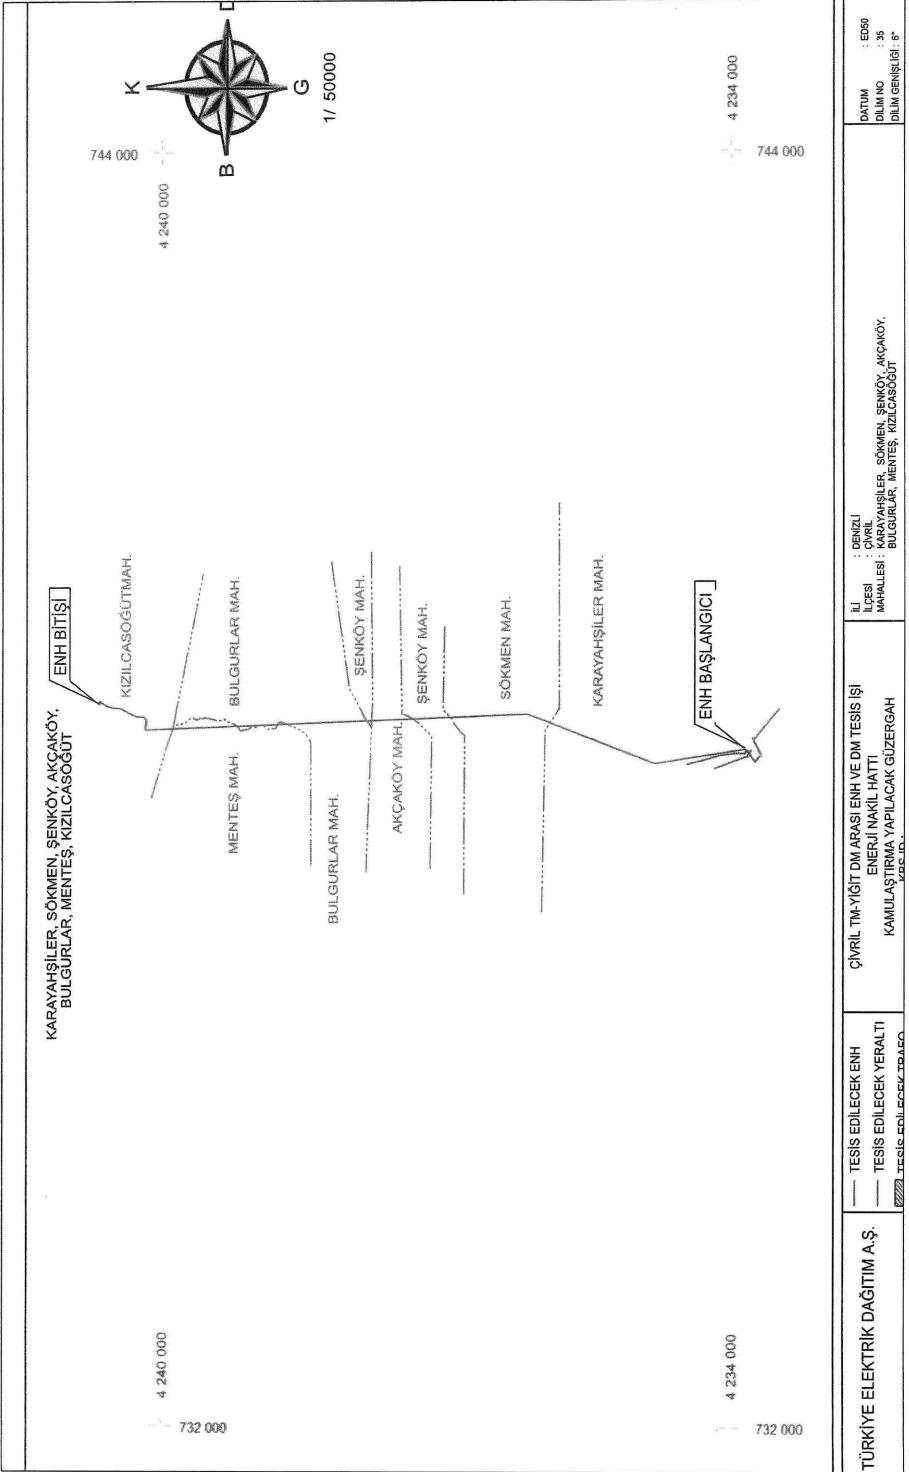

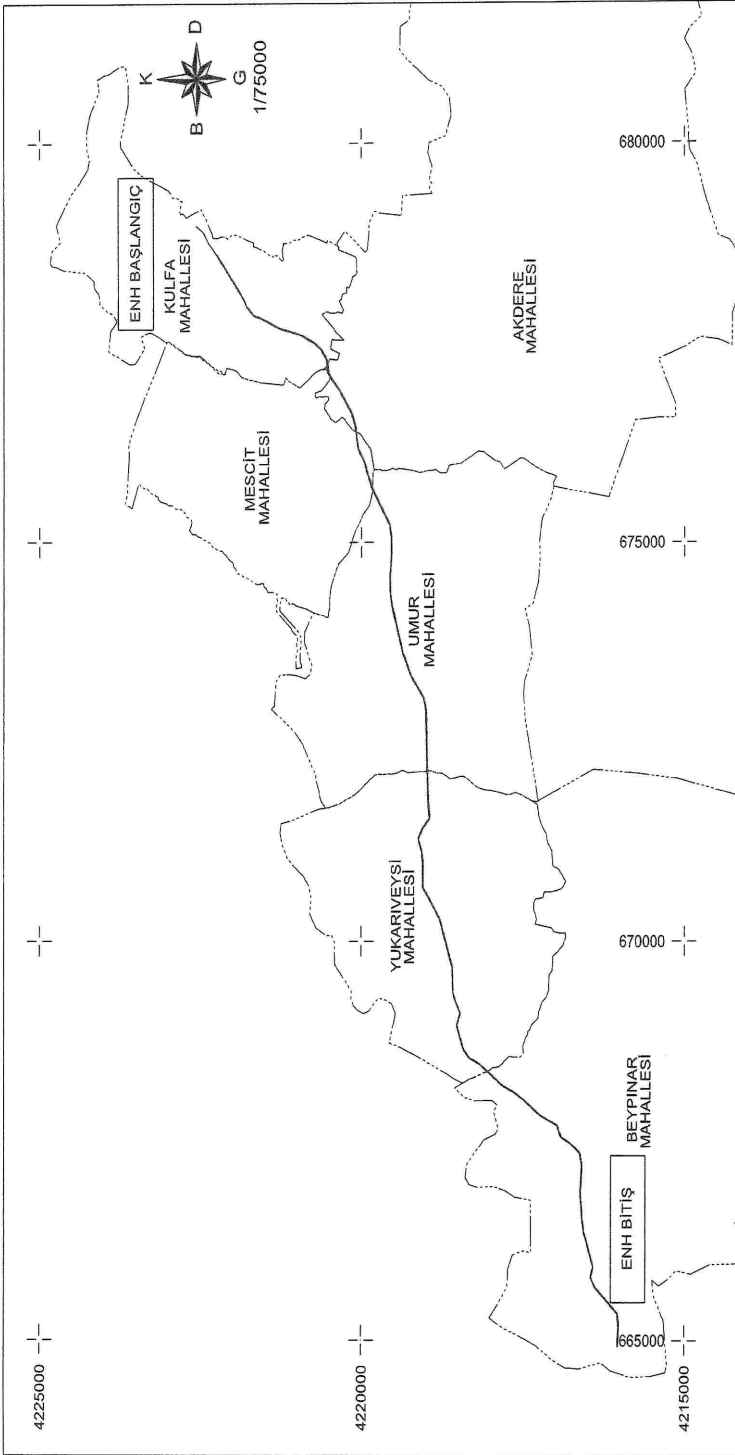

TÜRKİYE ELEKTRİK DAĞITIM A.Ş.		TESİS EDİLECEK ENH TESİS EDİLECEK YERALTI TESİS EDİLECEK TRAF0	NAZAR-SARKIYSAN GES ENH KAMULAŞTIRMA YAPILACAK GÜZERGAH	İL : İLÇE : MAHALLE :	DIYARBAKIR SİLVAN KULFA-MESCİT-UMUR-AKDERE YUKARIVEYSİ-BEYPINAR	DATUM : ED-50 D.O.M : 39 DİLM GENİŞLİĞİ : 6 PAFTA : L45 - L46
-------------------------------	---	--	--	-----------------------------	--	--

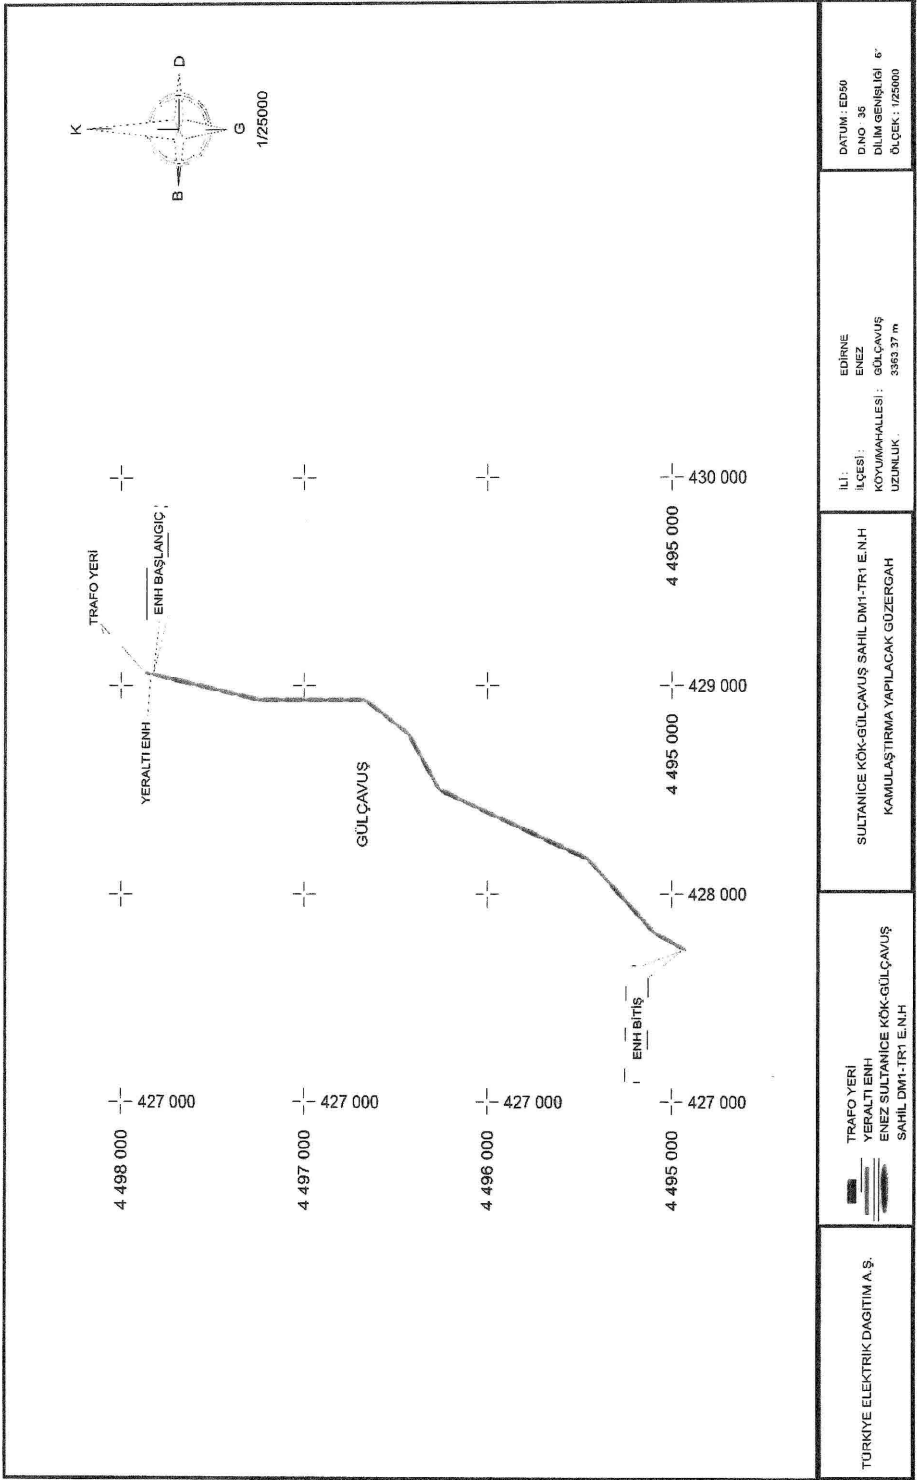


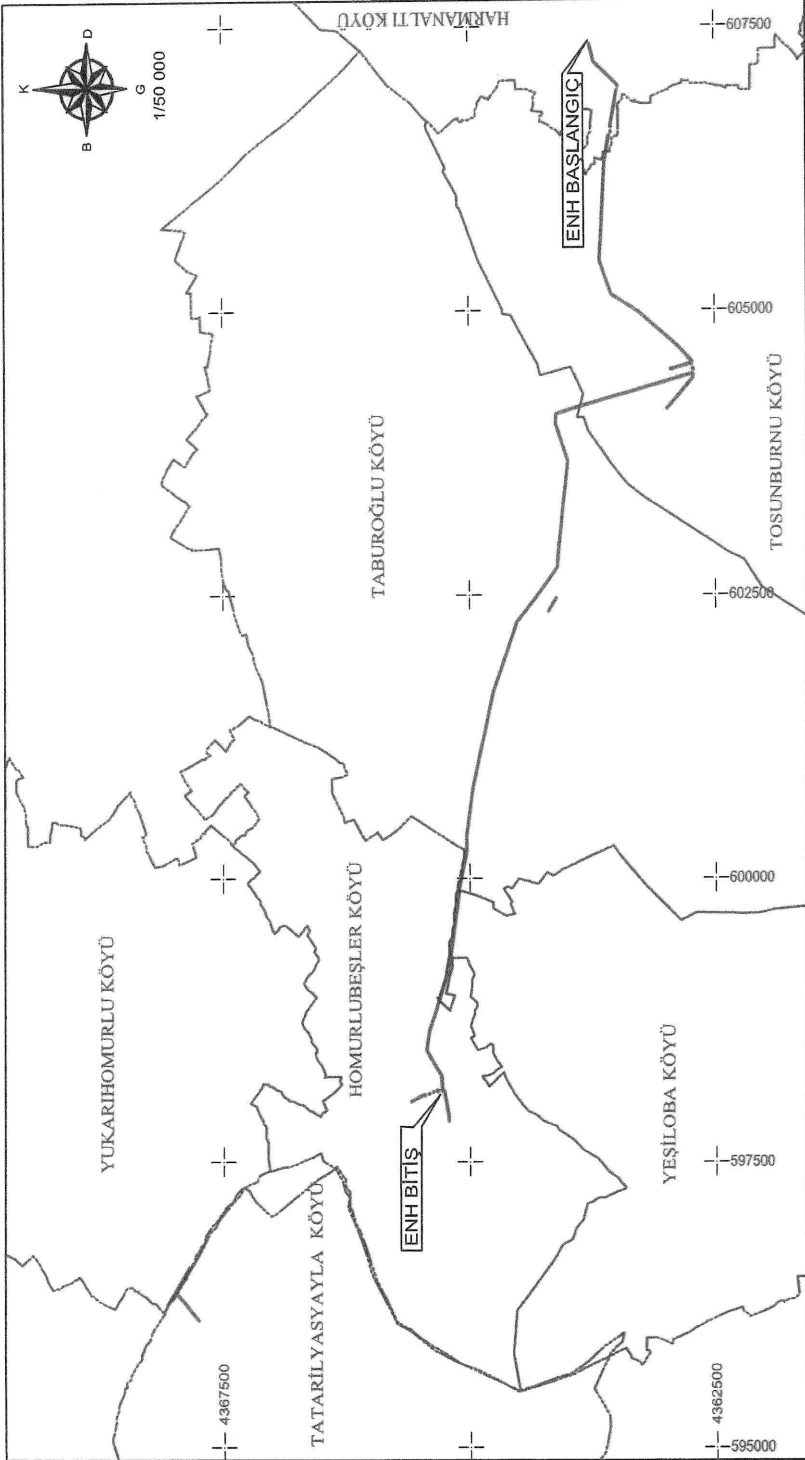


DATUM : ED50 D.NO : 36 DİLİM ARAĞI : 6° DİLİM ARAĞI : J32A1-J32A2	İL : KIRŞEHİR İLÇESİ: BOZTEPE VE MERKEZ KÖY : HARMANALTI, TOSUNBURNU, TABUROĞLU, YEŞİLOBA, HOMURLUBEŞLER, YUKARIHOMURLU VE TATARILYASYAYLA	TESİS EDİLECEK ENH TESİS EDİLECEK YERLER TESİS EDİLECEK TRAFİ	TÜRKİYE ELEKTRİK DAĞITIM A.Ş.
--	---	--	--------------------------------------




TÜRKİYE ELEKTRİK DAĞITIM A.Ş.	TESİS EDİLECEK ENH TESİS EDİLECEK YERALTI TESİS EDİLECEK TRAFİ	66 NOLU KÖK - SARNIÇ DM ENERJİ NAKİL HATTI KAMULAŞTIRMA YAPILACAK GÜZERGAH KBS ID: 101853	İL: KONYA İLÇESİ: ALTINEKİN MAHALLESİ: ÖLMEZ KÖYÜ, SARNIÇ	DATUM : ED50 D.NO : 36 DİLİM ARALIĞI : 6° PAFTA : L29-B4, L29-C1
-------------------------------	---	---	--	---

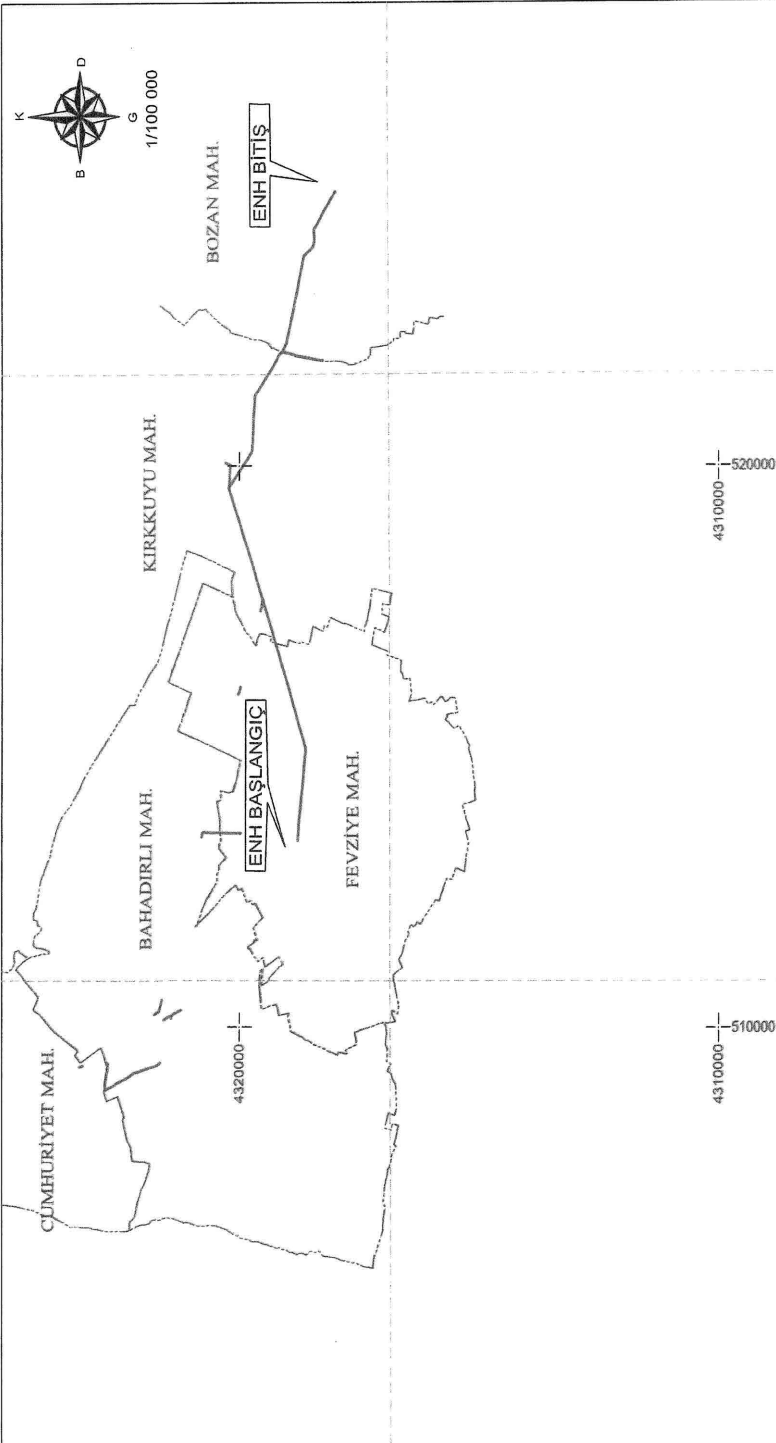


TÜRKİYE ELEKTRİK DAĞITIM A.Ş.	TESİS EDİLECEK ENH TESİS EDİLECEK YERALTI TESİS EDİLECEK TRAFİ	FEVZİYE KÖK BOZAN ENERJİ NAKİL HATTI KAMULAŞTIRMA YAPILACAK GÜZERGAH KBS ID: 101877	İL: KONYA İLÇESİ: KULU MAHALLE: CUMHURİYET, BAHADIRLI, FEVZİYE, KIRKKUYU, BOZAN	DATUM : ED50 D.NO : 36 DİLİM ARALIĞI : 6° PAFTA : J30-D4, J30-D3 PAFTA : J30-C4
-------------------------------	---	--	---	---

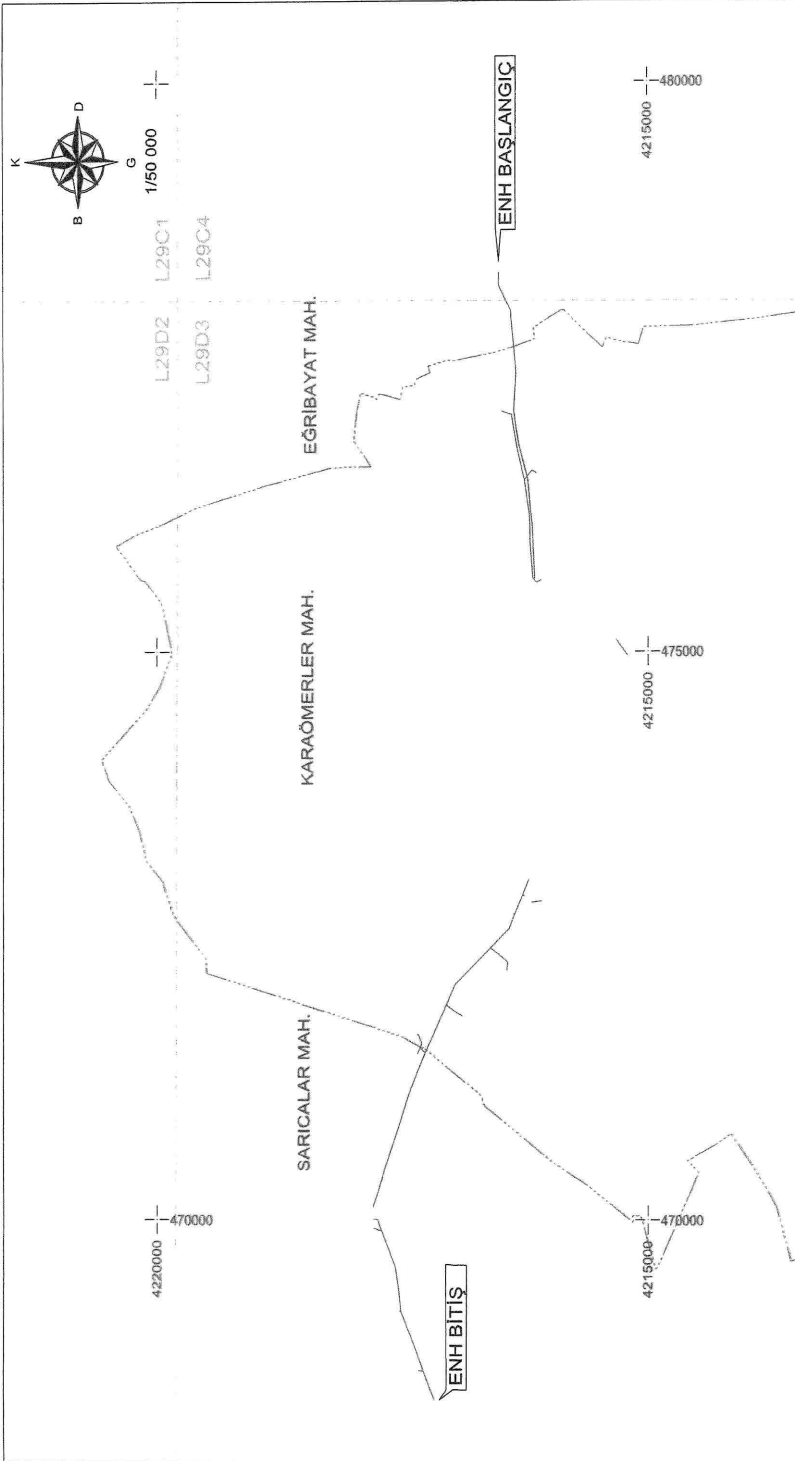


DATUM : ED50 D.NO : 36 DİLİM ARALIĞI : 6° PAFTA : L29D3.L29C4	İLİ: KONYA İLÇESİ: SELÇUKLU MAHALLE: KARAOEMERLER, SARICALAR,EĞRİBAYAT	KARAOEMERLER DM ENERJİ NAKİL HATTI KAMULAŞTIRMA YAPILACAK GÜZERGAH KBS ID: 102581	TESİS EDİLECEK ENH TESİS EDİLECEK YERALTI TESİS EDİLECEK TRAFİ	TÜRKİYE ELEKTRİK DAĞITIM AŞ.
--	---	--	---	-------------------------------------

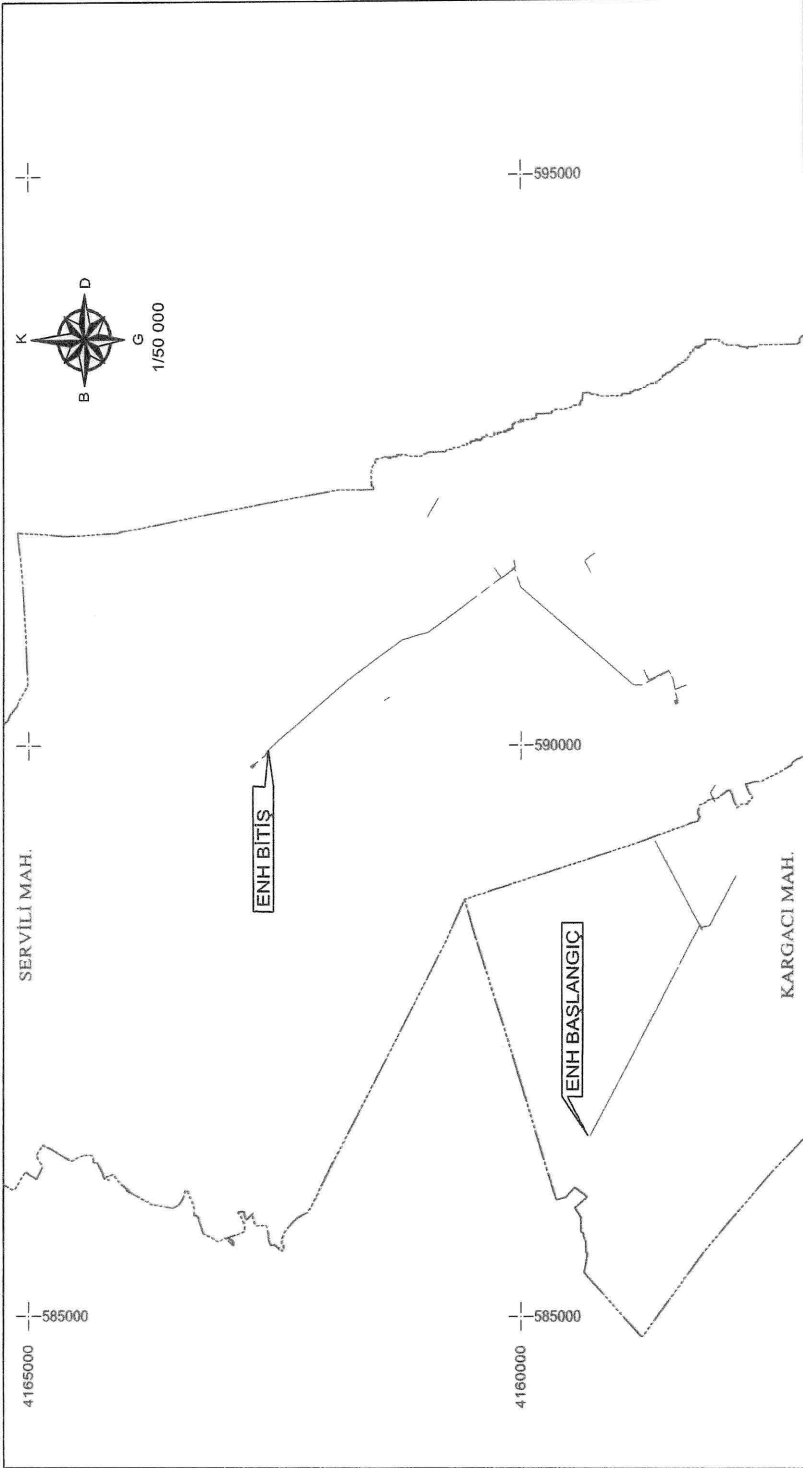


DATUM : ED50 D.NO : 36 DİLİM ARALIĞI : 6° PAFTA : M31C3.M32D4	İLİ: KONYA İLÇESİ: EREĞLİ MAHALLE: KARGACI, SERVİLİ	KARGACI SERVİLİ PINARÖZÜ ENERJİ NAKİL HATTI KAMULAŞTIRMA YAPILACAK GÜZERGAH KBS ID: 102552	TESİS EDİLECEK ENH TESİS EDİLECEK YERALTI TESİS EDİLECEK TRAFİ	TÜRKİYE ELEKTRİK DAĞITIM AŞ.
--	--	---	---	-------------------------------------

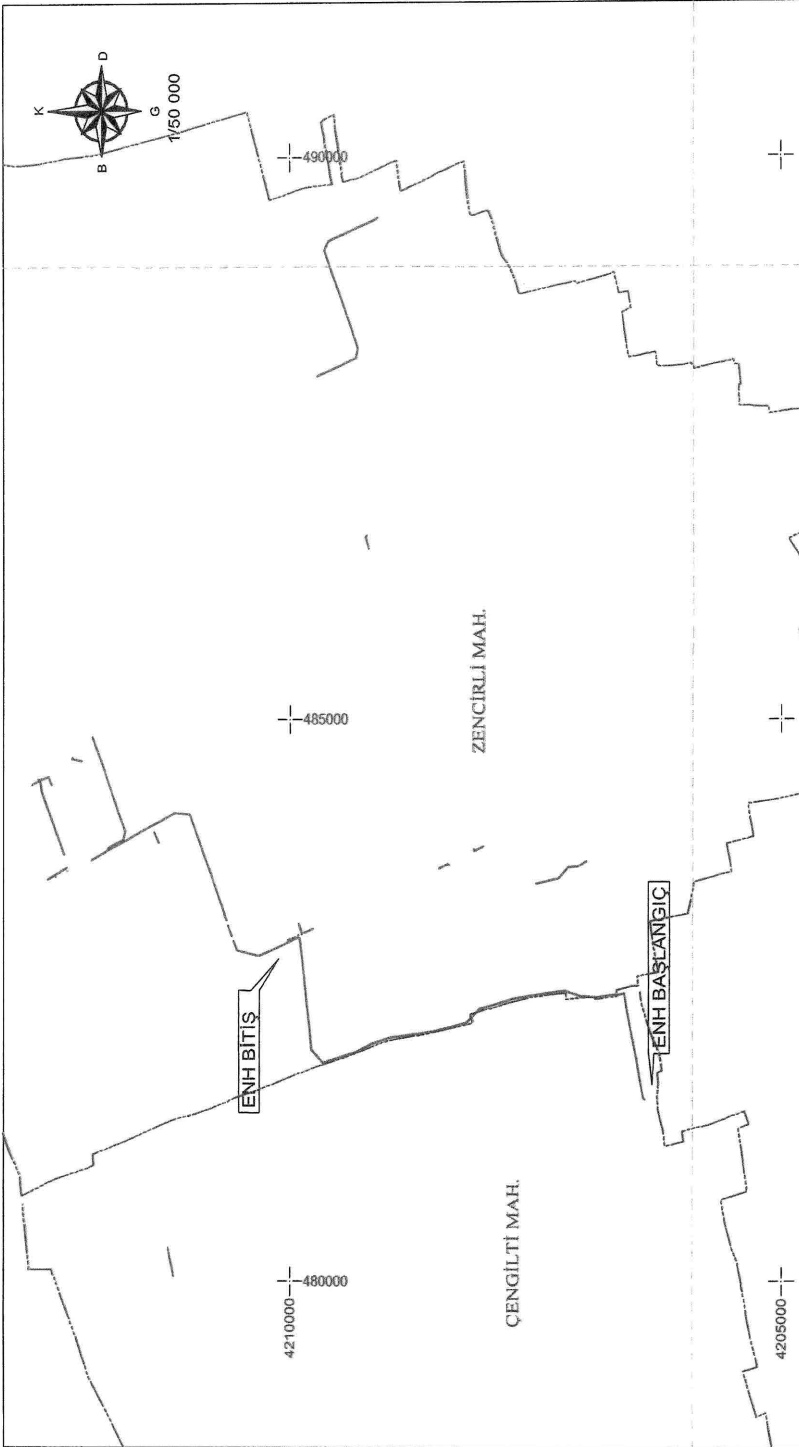


TÜRKİYE ELEKTRİK DAĞITIM AŞ.	TESİS EDİLECEK ENİH TESİS EDİLECEK YERALTI TESİS EDİLECEK TRAFO	ZİNCİRLİ SULAMA ENERJİ NAKİL HATTI KAMULAŞTIRMA YAPILACAK GÜZERGAH KBS ID: 102575	İLİ: KONYA İLÇESİ: KARATAY MAHALLE: ÇENGİLTİ, ZENCİRLİ	DATUM : ED50 D.NO : 36 DİLİM ARALIĞI : 6° PAFTA : L29-C4, L29-C3
-------------------------------------	--	--	---	---

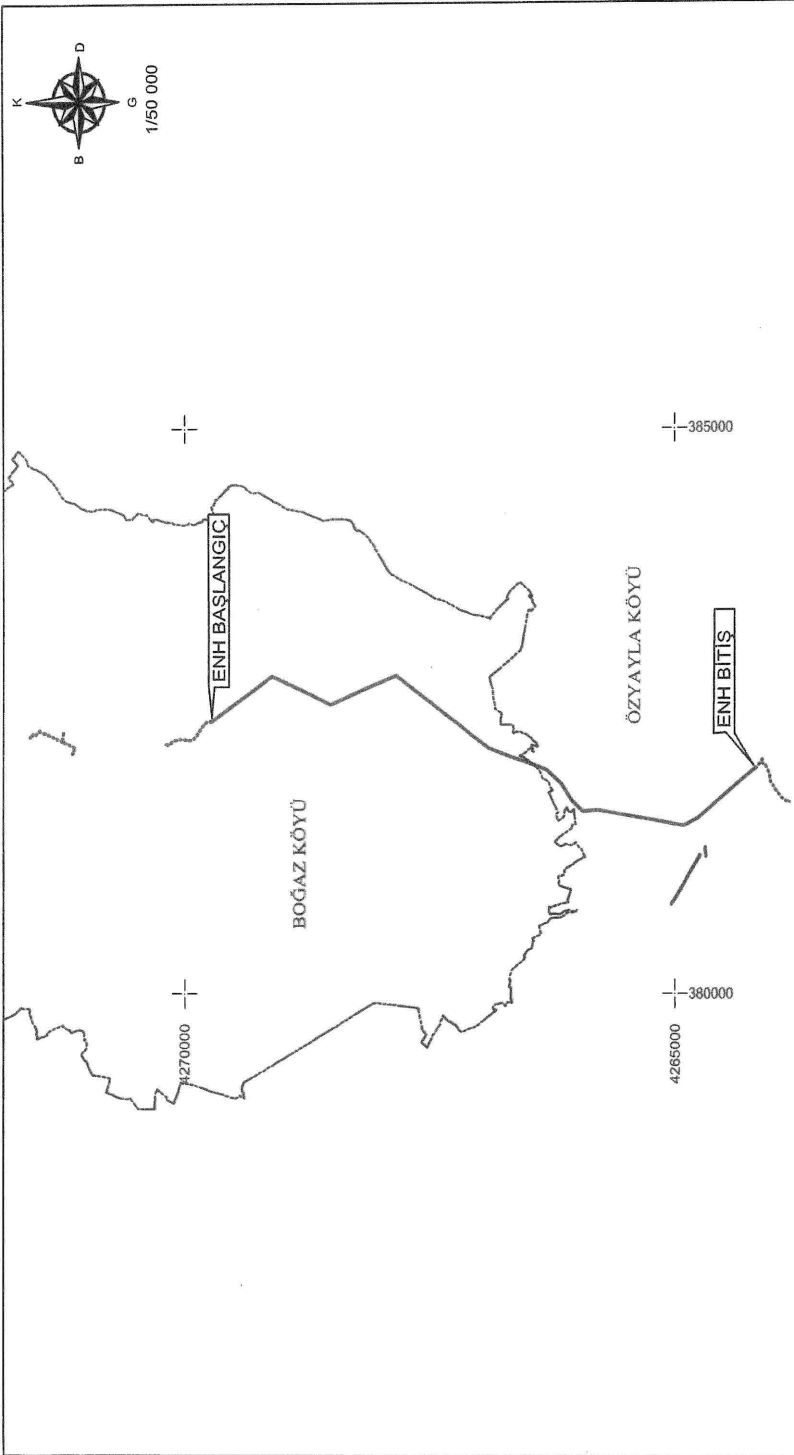


TÜRKİYE ELEKTRİK DAĞITIM AŞ	TESİS EDİLECEK ENH TESİS EDİLECEK YERALTI TESİS EDİLECEK TRAFİ	BOĞAZ ADM VE İRTİBATLARI ENERJİ NAKİL HATTI KAMULAŞTIRMA YAPILACAK GÜZERGAH KBS ID: 101802	İLİ: NEVŞEHİR İLÇESİ: MERKEZ KÖY: BOĞAZ VE ÖZYAYLA	DATUM : ED50 D.NO : 36 DİLİM ARA LIĞI : 6° PAFTA : K33D3 - L33A2
------------------------------------	---	---	---	---

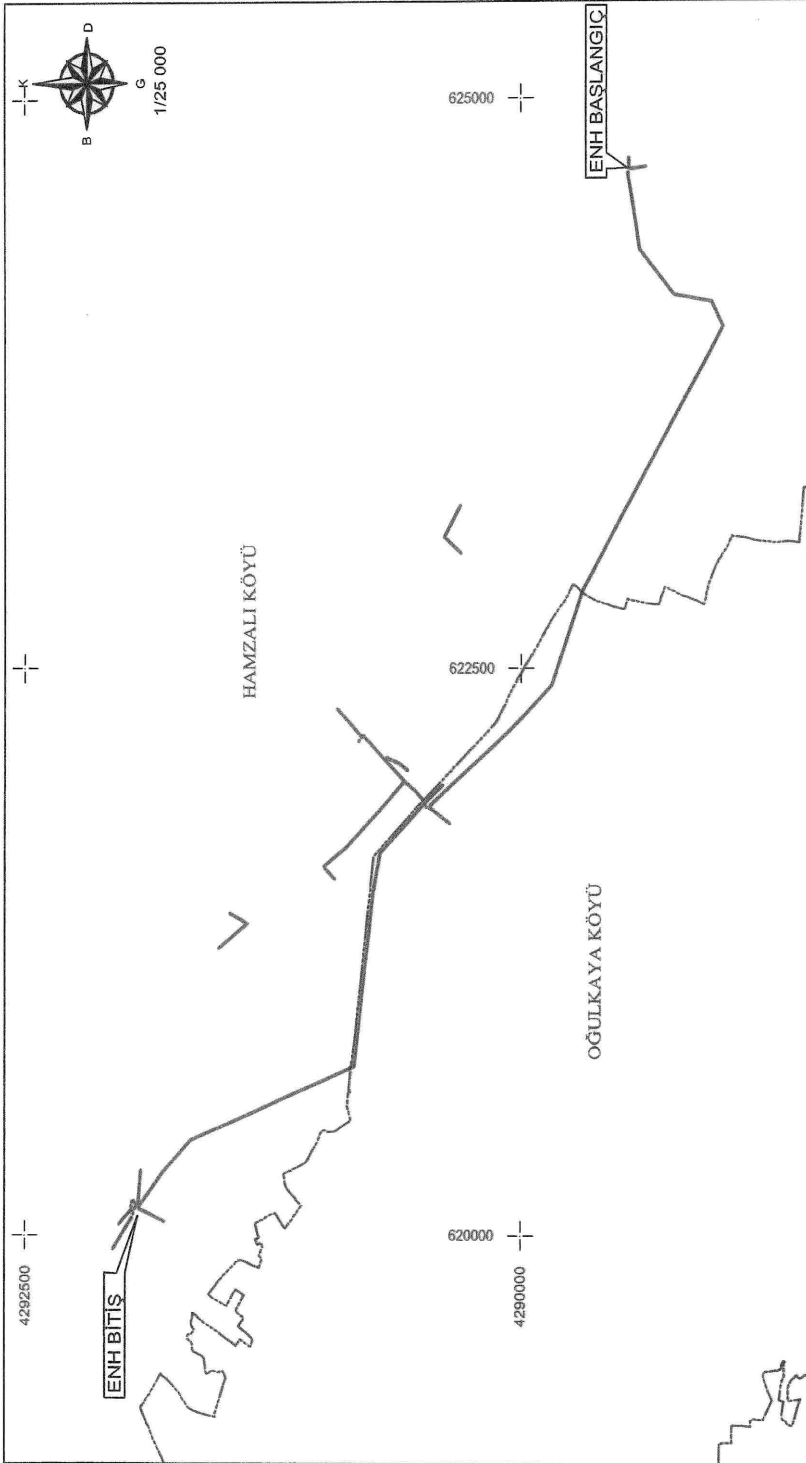



DATUM : ED50 D.NO : 36 DİLİM ARALIĞI : 6° SAFTA : K32B3 - K32C2	İLİ: NEVŞEHİR İLÇESİ: GÜLŞEHİR KÖY: HAMZALI VE OĞULKAYA	HAMZALI GES KÖK-HAMZALI MOD ENERJİ NAKİL HATTI KAMULAŞTIRMA YAPILACAK GÜZERGAH KBS ID:102574	TESİS EDİLECEK ENH TESİS EDİLECEK YERALTI TESİS EDİLECEK TRAFİ	TÜRKİYE ELEKTRİK DAĞITIM AŞ
---	--	--	---	------------------------------------

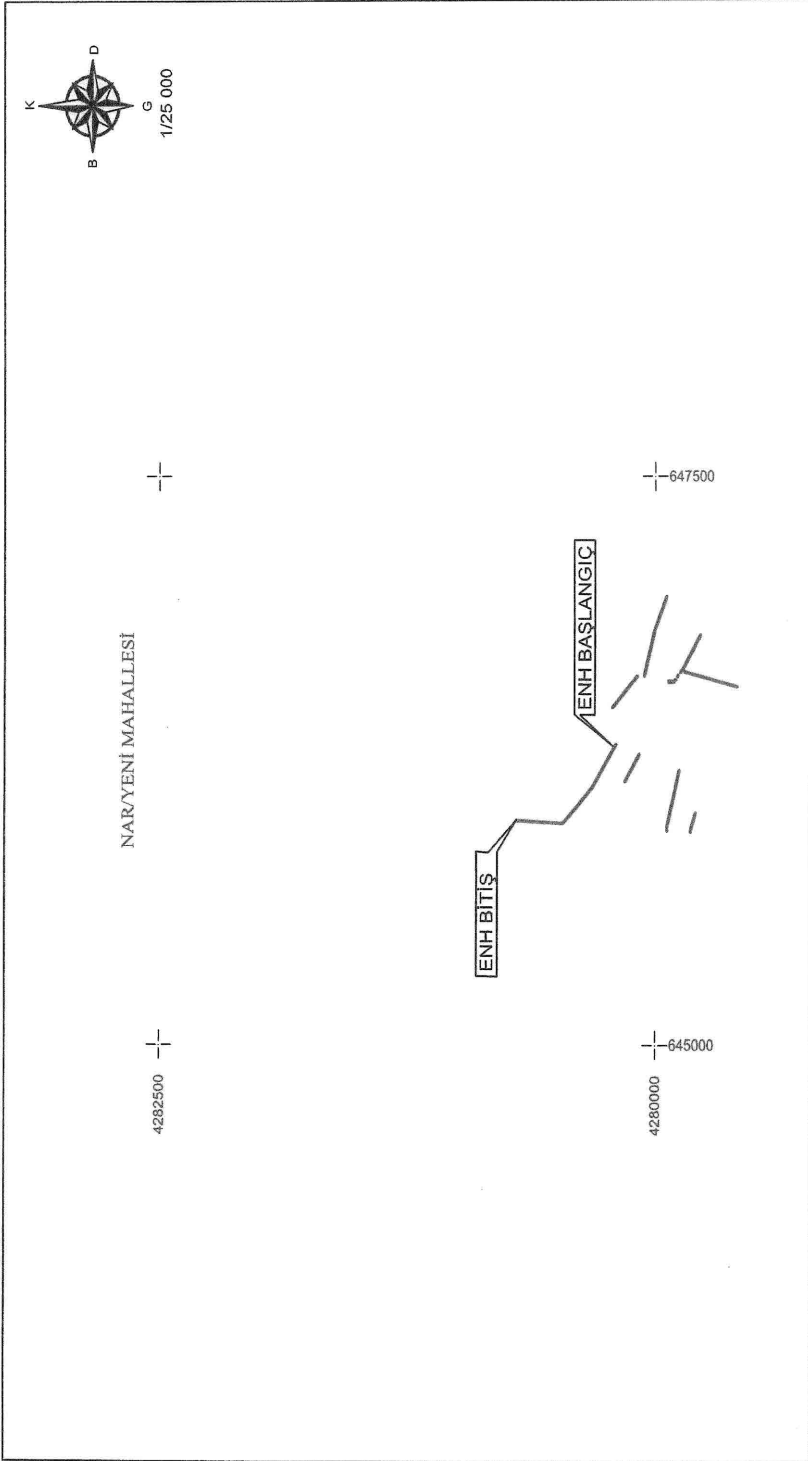

TÜRKİYE ELEKTRİK DAĞITIM AŞ.	TESİS EDİLECEK ENH TESİS EDİLECEK YERALTI TESİS EDİLECEK TRAFİ	ÖZAY İM VE İRTİBATLARI ENERJİ NAKİL HATTI KAMULAŞTIRMA YAPILACAK GÜZERGAH KBS ID:101486	İL: NEVŞEHİR İLÇESİ: MERKEZ MAHALLE: NAR/YENİ	DATUM : ED50 D.NO : 36 DİLİM ARALIĞI : 6° PAFTA : K33-D2
-------------------------------------	---	---	--	--

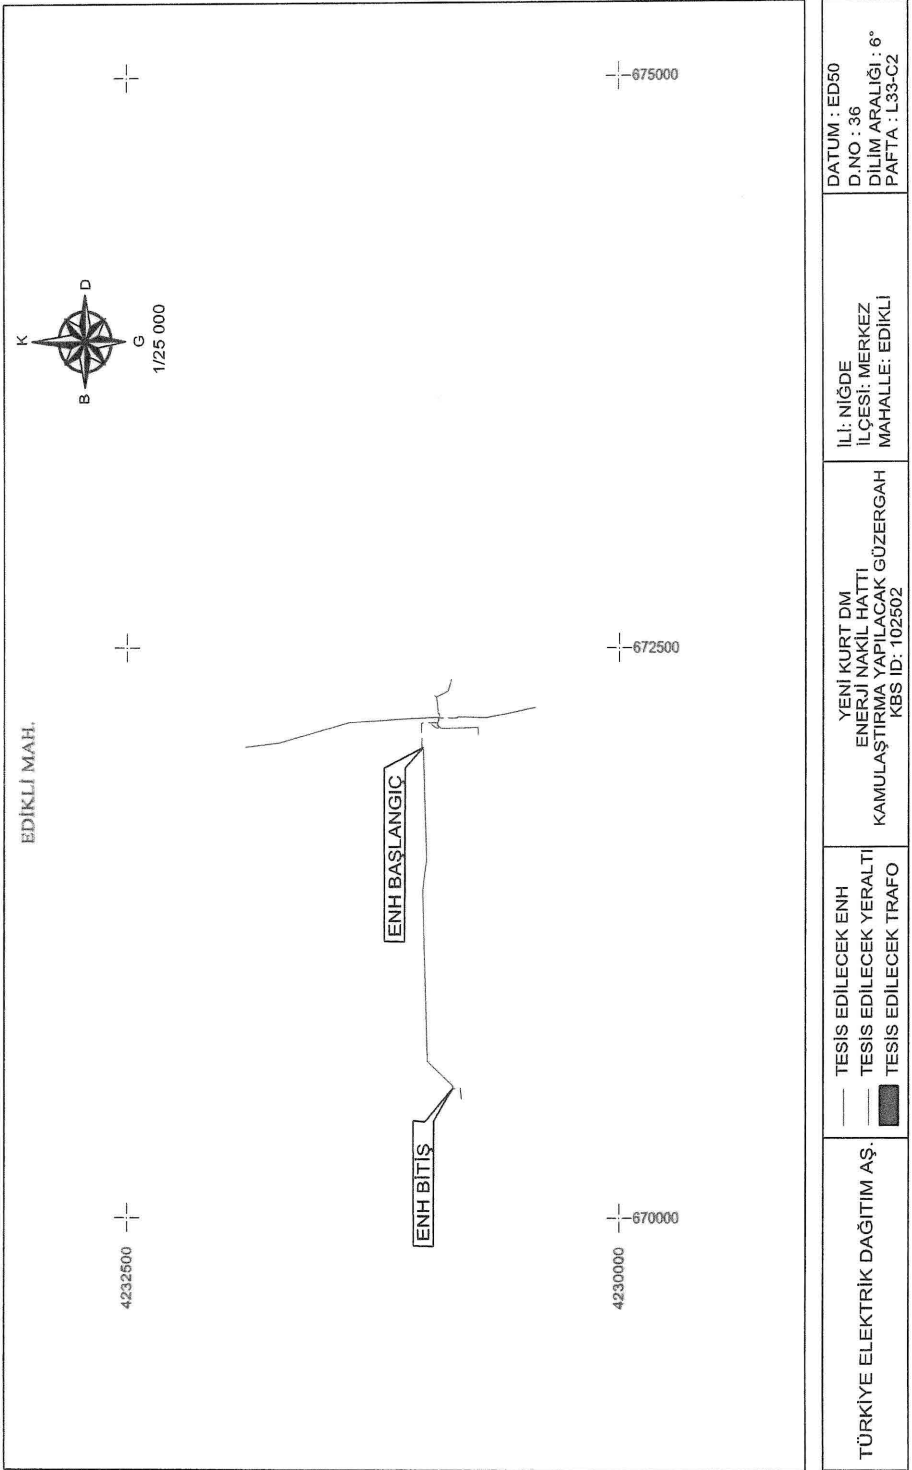

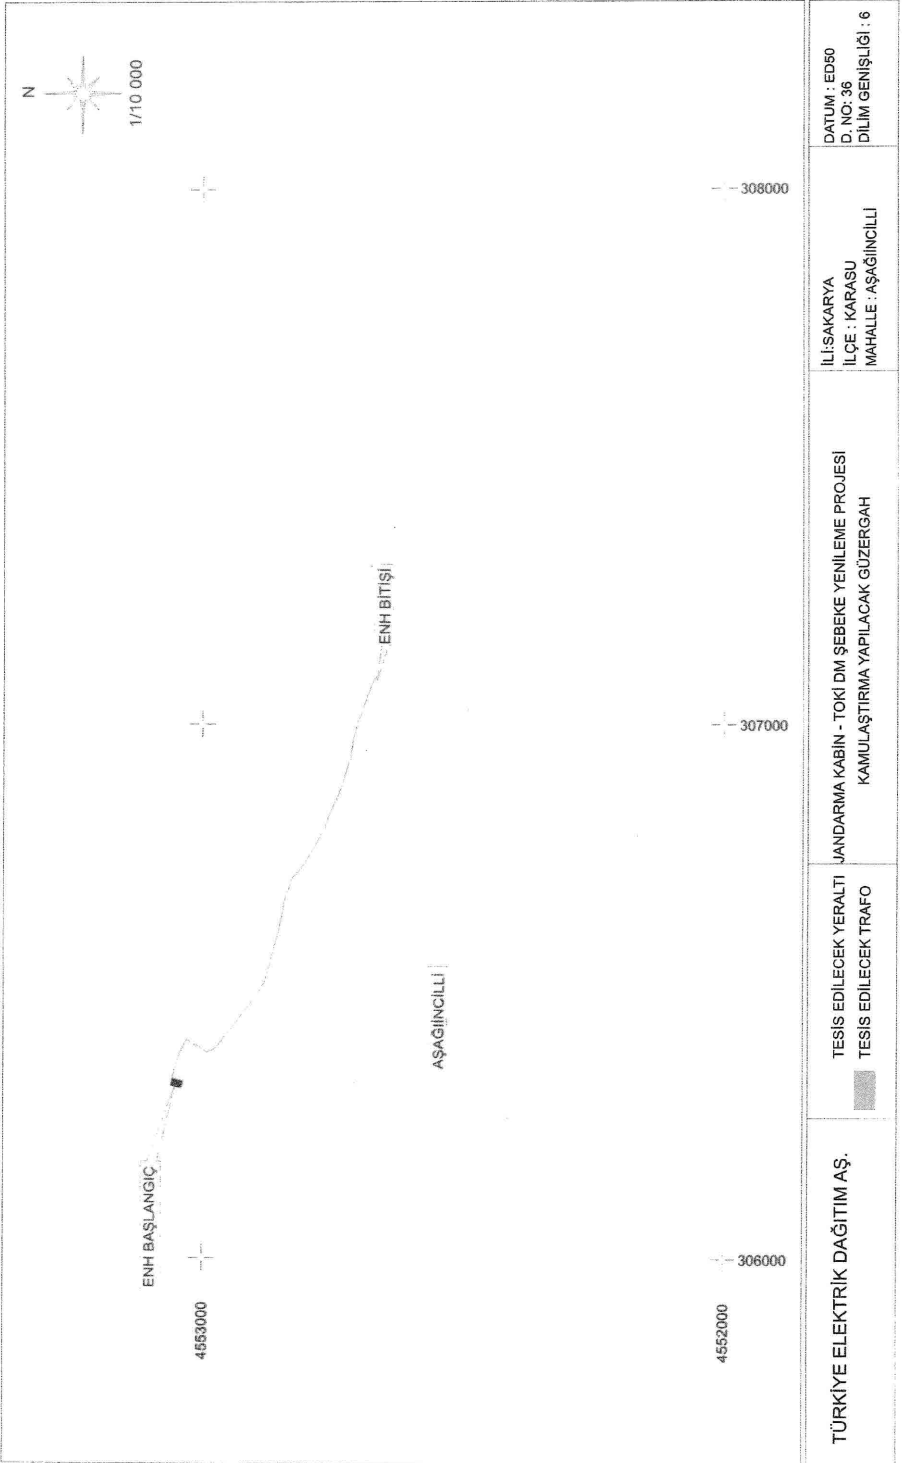

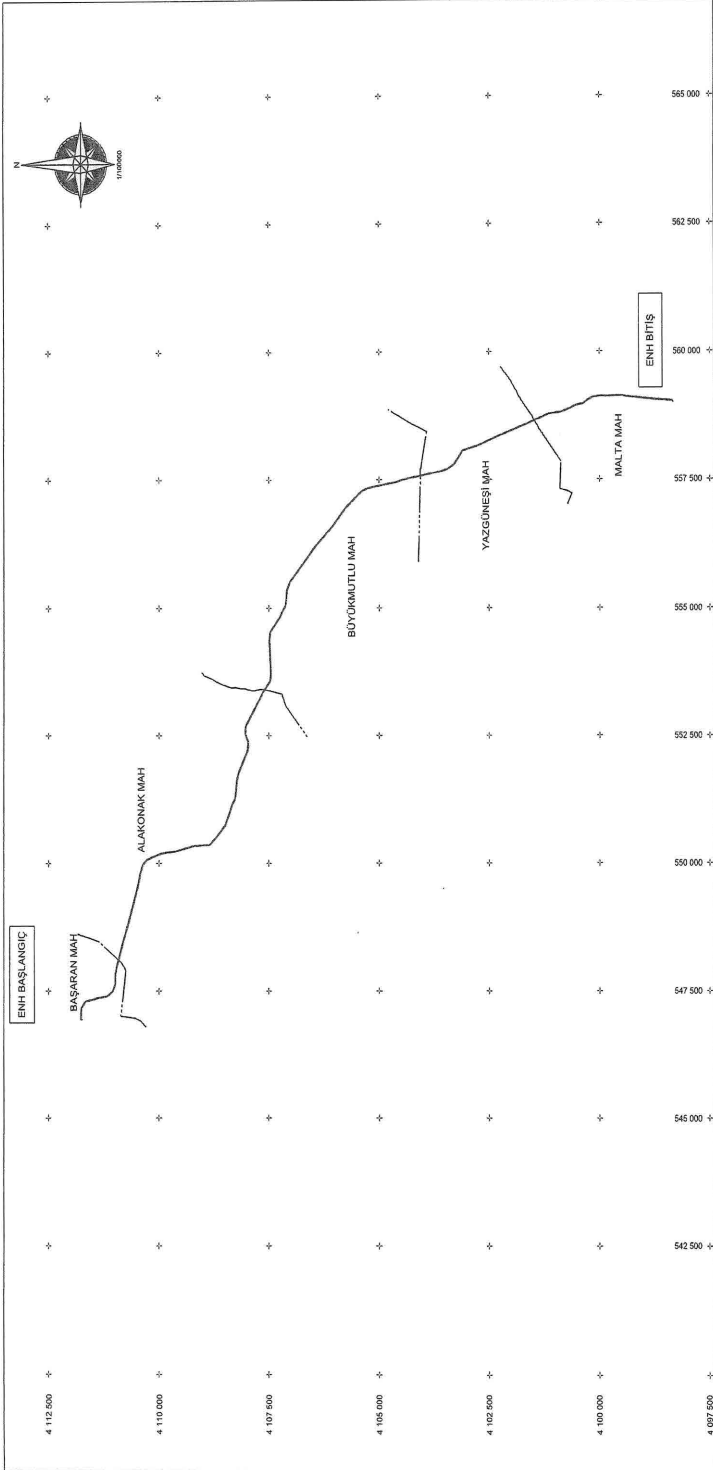

DATUM : ED50
D.O.M : 39
DİLİM GENİŞLİĞİ : 6°

İLİ:ŞANLIURFA
İLÇESİ: VİRANŞEHİR
MAHALLE: BAŞARAN, ALAKONAK
BÜYÜKMUTLU, YAZGÜNEŞİ,
MALTA

BİM VİRANŞEHİR GES ENH
KAMULAŞTIRMA YAPILACAK GÜZERGAH

TESİS EDİLECEK TRAFO
TESİS EDİLECEK ENH
TESİS EDİLECEK YERALTI



TÜRKİYE ELEKTRİK DAĞITIM A.Ş.

